

# CORNER RECORD

Agency Index


Document Number

2019-0511

City of SANTA ANA

County of ORANGE, California

Brief Legal Description CENTERLINE INTERSECTION OF BEWLEY STREET AND 11TH STREET

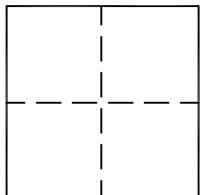

## CORNER TYPE

- Government Corner       Control
- Meander       Property
- Rancho       Other

## COORDINATES (Optional )

N. \_\_\_\_\_ E. \_\_\_\_\_  
 Elevation \_\_\_\_\_  
 Units \_\_\_\_\_ Metric \_\_\_\_\_ U.S. Survey Foot \_\_\_\_\_  
 Horizontal Datum \_\_\_\_\_  
 Zone \_\_\_\_\_ Epoch Date \_\_\_\_\_  
 Vertical Datum \_\_\_\_\_

Date of Survey JULY 18, 2018

- Complies with Public Resources Code §§8801-8819
- Complies with Public Resources Code §§8890-8902

PLS Act Ref:  8765(d)       8771       8773       Other:

Corner/ Monument:	<input checked="" type="checkbox"/> Left as found	<input type="checkbox"/> Established	<input type="checkbox"/> Rebuilt	<input checked="" type="checkbox"/> Pre-Construction
	<input type="checkbox"/> Found and tagged	<input type="checkbox"/> Reestablished	<input type="checkbox"/> Referenced	<input type="checkbox"/> Post-Construction

Narrative of corner identified and monument as found, set, reset, replaced, or removed:

See sheet #2 for description (s):

*THESE TIES ARE FOR THE PURPOSE OF PERPETUATING THE FOUND MONUMENTATION. NO CLAIM IS MADE AS TO THE RELATIONSHIP OF THE POINTS OR LINES SHOWN HEREON TO THE TRUE BOUNDARY LOCATIONS.*

## SURVEYOR'S STATEMENT

This Corner Record was prepared by me or under my direction in conformance with  
the Professional Land Surveyors' Act on SEPTEMBER 17, 2019

Signed Jeffrey J. Lenherr P.L.S. or R.C.E. No. 9305



## COUNTY SURVEYOR'S STATEMENT

This Corner Record was received FEB 4 2019


and examined and filed SEP 27 2019

Signed Kevin R. Hills P.L.S. or R.C.E. No. 6617

Title COUNTY SURVEYOR



County Surveyor's Comment \_\_\_\_\_  
 \_\_\_\_\_  
 \_\_\_\_\_

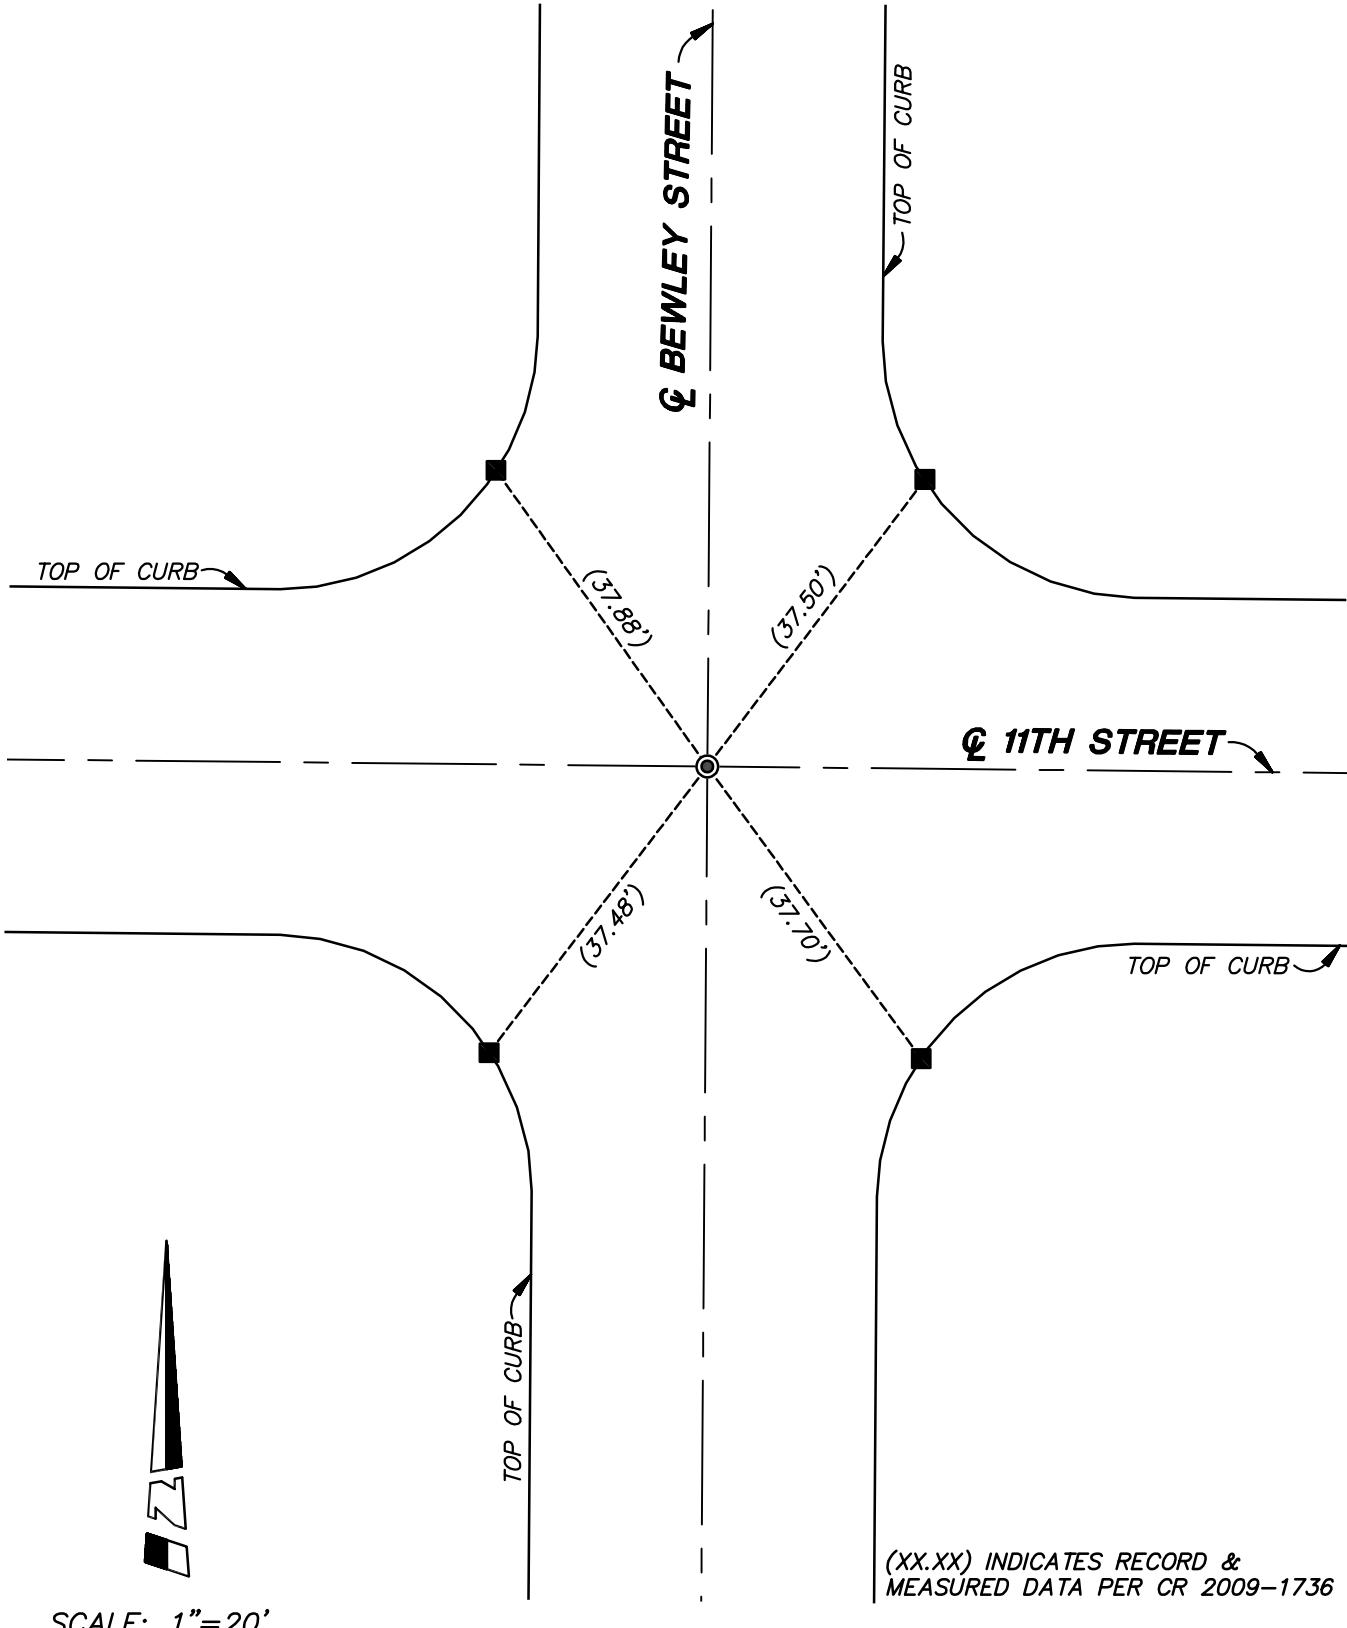

### MONUMENT NOTES

NOTE: THESE TIES ARE FOR THE PURPOSE  
OF PERPETUATING THE FOUND  
MONUMENTATION. NO CLAIM IS MADE AS TO  
THE RELATIONSHIP OF THE POINTS OR LINES  
SHOWN HEREON TO THE TRUE BOUNDARY  
LOCATIONS.

- FOUND CHISELED "X" ON TOP OF CURB PER CR 2009-1736,  
SET LEAD, TACK & TAG "PLS 9305 TIE"
- FOUND NOTHING, RE-ESTABLISHED INTERSECTION ON SEWER  
MANHOLE COVER PER CR 2009-1736

# CORNER RECORD

Agency Index


Document Number

2019-0515

City of SANTA ANA

County of ORANGE, California

Brief Legal Description CENTERLINE INTERSECTION OF JACKSON STREET AND LINCOLN WAY AND  
THE CUL-DE-SAC ON LINCOLN WAY EAST OF JACKSON STREET

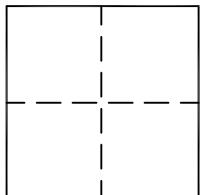

## CORNER TYPE

## COORDINATES (Optional )

- Government Corner       Control
- Meander       Property
- Rancho       Other

N. \_\_\_\_\_ E. \_\_\_\_\_

Elevation \_\_\_\_\_

Units \_\_\_\_\_ Metric  U.S. Survey Foot

Horizontal Datum \_\_\_\_\_

Zone \_\_\_\_\_ Epoch Date \_\_\_\_\_

Vertical Datum \_\_\_\_\_

Date of Survey JULY 18, 2018

Complies with Public Resources Code §§8801-8819

Complies with Public Resources Code §§8890-8902

PLS Act Ref:  8765(d)       8771       8773       Other:

Corner/ Monument:	<input checked="" type="checkbox"/> Left as found	<input type="checkbox"/> Established	<input type="checkbox"/> Rebuilt	<input checked="" type="checkbox"/> Pre-Construction
	<input type="checkbox"/> Found and tagged	<input type="checkbox"/> Reestablished	<input type="checkbox"/> Referenced	<input type="checkbox"/> Post-Construction

Narrative of corner identified and monument as found, set, reset, replaced, or removed:

See sheet #2 for description (s):

*THESE TIES ARE FOR THE PURPOSE OF PERPETUATING THE FOUND MONUMENTATION. NO CLAIM IS MADE AS TO THE RELATIONSHIP OF THE POINTS OR LINES SHOWN HEREON TO THE TRUE BOUNDARY LOCATIONS.*

## SURVEYOR'S STATEMENT

This Corner Record was prepared by me or under my direction in conformance with

the Professional Land Surveyors' Act on SEPTEMBER 17, 2019

Signed Jeffrey J. Lenherr P.L.S. or R.C.E. No. 9305



## COUNTY SURVEYOR'S STATEMENT

**FEB 4 2019**

This Corner Record was received \_\_\_\_\_

**SEP 27 2019**


and examined and filed \_\_\_\_\_

Signed Kevin R. Hills P.L.S. or R.C.E. No. 6617

Title COUNTY SURVEYOR



County Surveyor's Comment \_\_\_\_\_  
\_\_\_\_\_  
\_\_\_\_\_

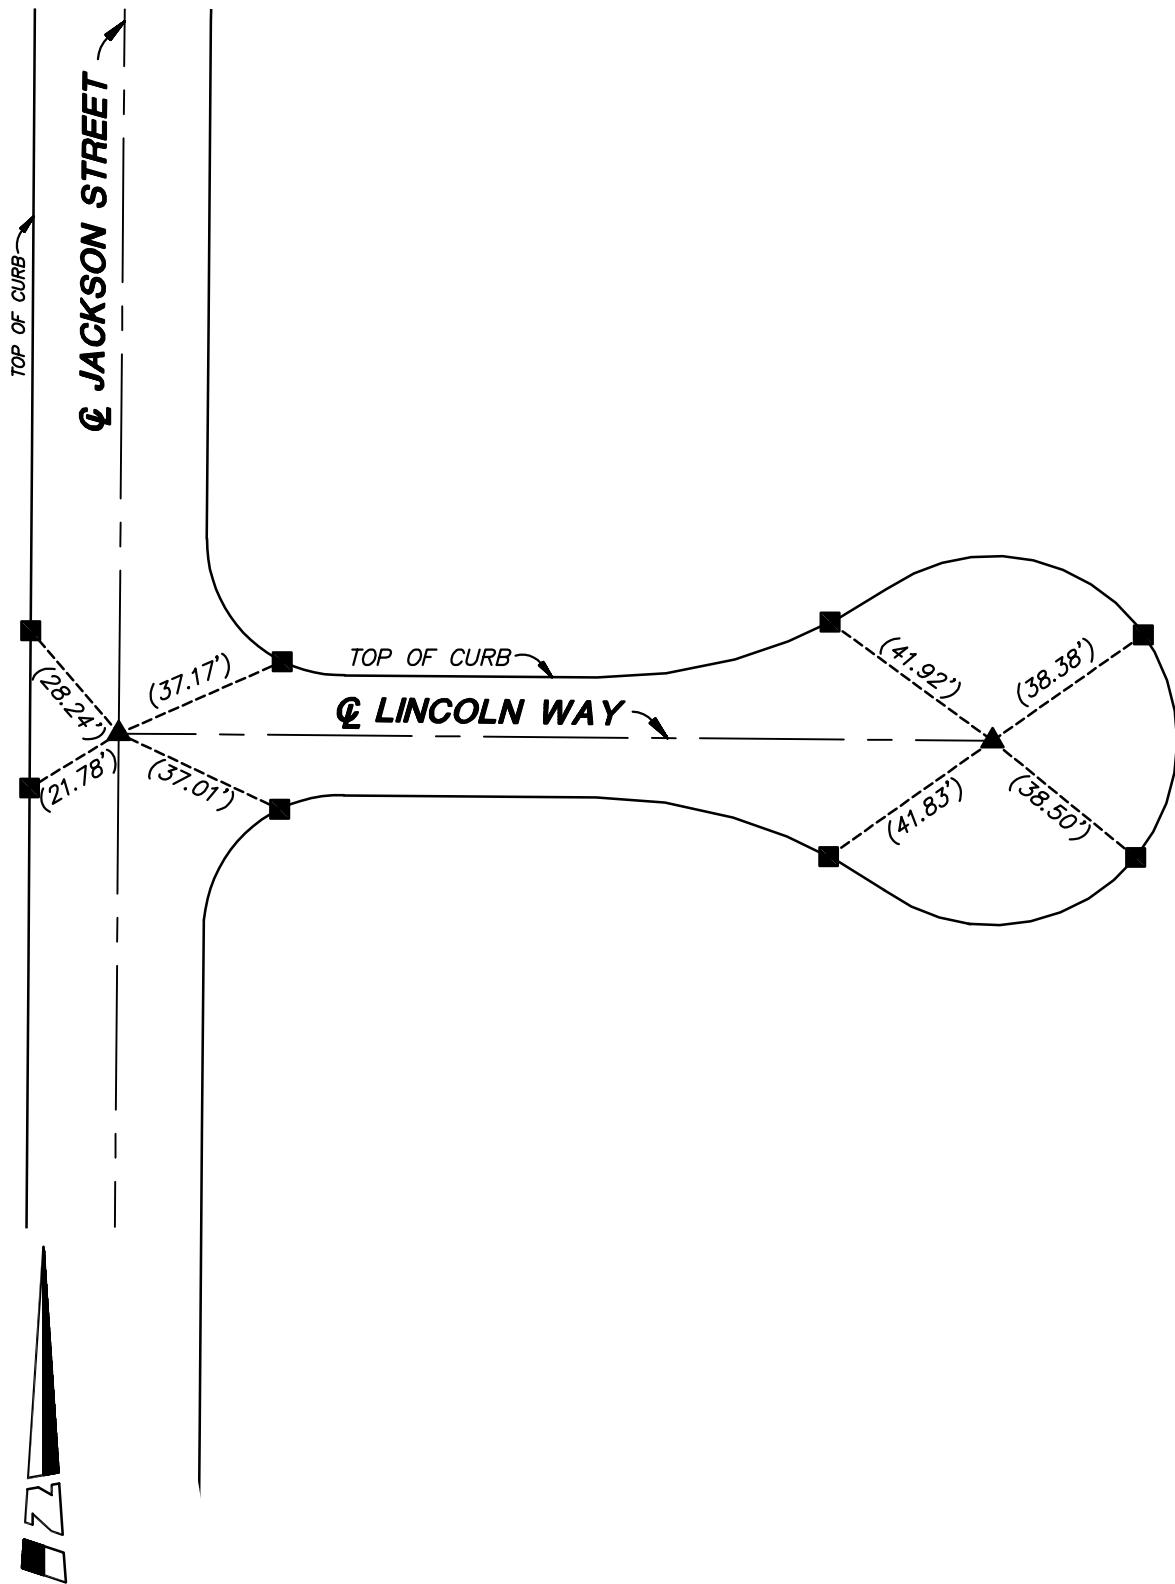

SCALE: 1"=40'

(XX.XX) INDICATES RECORD &amp; MEASURED DATA PER CR 2010-2713

### MONUMENT NOTES

NOTE: THESE TIES ARE FOR THE PURPOSE OF PERPETUATING THE FOUND MONUMENTATION. NO CLAIM IS MADE AS TO THE RELATIONSHIP OF THE POINTS OR LINES SHOWN HEREON TO THE TRUE BOUNDARY LOCATIONS.

- FOUND LEAD, TACK & TAG ON TOP OF CURB, STAMPED "LS 5848" PER CR 2010-2713
- ▲ FOUND GEAR SPIKE AND WASHER, STAMPED "LS 5848" PER CR 2010-2713, FLUSH

# CORNER RECORD

Agency Index


Document Number

2019-0580

City of SANTA ANA

County of ORANGE, California

Brief Legal Description CENTERLINE INTERSECTION OF JACKSON STREET AND  
WASHINGTON AVENUE

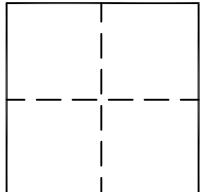

## CORNER TYPE

- Government Corner       Control
- Meander       Property
- Rancho       Other

## COORDINATES (Optional )

N. \_\_\_\_\_ E. \_\_\_\_\_  
 Elevation \_\_\_\_\_  
 Units \_\_\_\_\_ Metric \_\_\_\_\_ U.S. Survey Foot \_\_\_\_\_  
 Horizontal Datum \_\_\_\_\_  
 Zone \_\_\_\_\_ Epoch Date \_\_\_\_\_  
 Vertical Datum \_\_\_\_\_

Date of Survey JULY 18, 2018

- Complies with Public Resources Code §§8801-8819
- Complies with Public Resources Code §§8890-8902

PLS Act Ref:  8765(d)       8771       8773       Other:

Corner/ Monument:	<input checked="" type="checkbox"/> Left as found	<input type="checkbox"/> Established	<input type="checkbox"/> Rebuilt	<input checked="" type="checkbox"/> Pre-Construction
	<input type="checkbox"/> Found and tagged	<input type="checkbox"/> Reestablished	<input type="checkbox"/> Referenced	<input type="checkbox"/> Post-Construction

Narrative of corner identified and monument as found, set, reset, replaced, or removed:

See sheet #2 for description (s):

*THESE TIES ARE FOR THE PURPOSE OF PERPETUATING THE FOUND MONUMENTATION. NO CLAIM IS MADE AS TO THE RELATIONSHIP OF THE POINTS OR LINES SHOWN HEREON TO THE TRUE BOUNDARY LOCATIONS.*

## SURVEYOR'S STATEMENT

This Corner Record was prepared by me or under my direction in conformance with  
the Professional Land Surveyors' Act on SEPTEMBER 17, 2019

Signed Jeffrey J. Lenherr P.L.S. or R.C.E. No. 9305



## COUNTY SURVEYOR'S STATEMENT

**FEB 4 2019**

This Corner Record was received \_\_\_\_\_


and examined and filed SEP 27 2019

Signed Kevin R. Hills P.L.S. or R.C.E. No. 6617

Title COUNTY SURVEYOR



County Surveyor's Comment \_\_\_\_\_  
 \_\_\_\_\_  
 \_\_\_\_\_

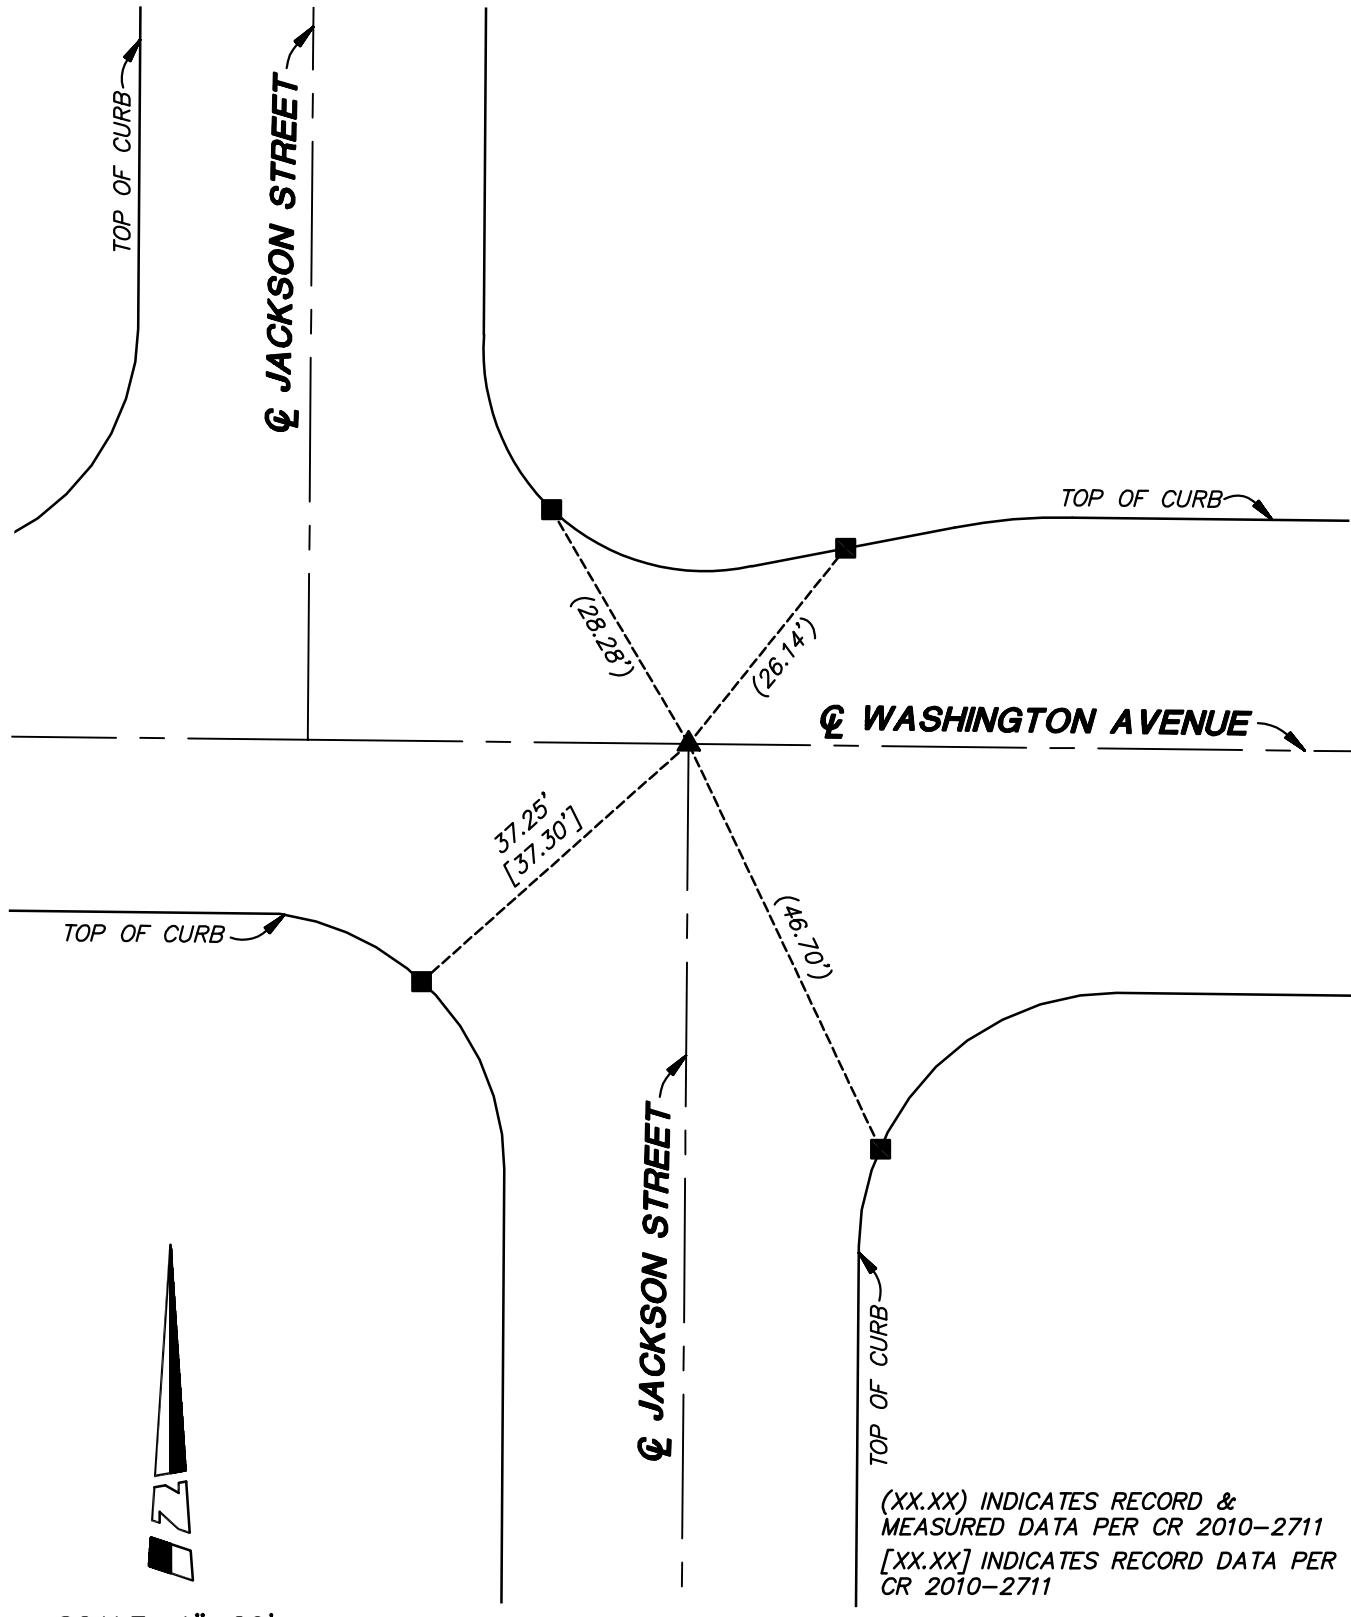

SCALE: 1"=20'

NOTE: THESE TIES ARE FOR THE PURPOSE OF PERPETUATING THE FOUND MONUMENTATION. NO CLAIM IS MADE AS TO THE RELATIONSHIP OF THE POINTS OR LINES SHOWN HEREON TO THE TRUE BOUNDARY LOCATIONS.

### MONUMENT NOTES

- FOUND CHISELED "X" ON TOP OF CURB PER CR 2010-2711, SET LEAD, TACK & TAG "PLS 9305 TIE"
- ▲ FOUND GEAR SPIKE AND WASHER, STAMPED "LS 5848" PER CR 2010-2711, DOWN 0.1'

# CORNER RECORD

Agency Index


Document Number

2019-0581

City of SANTA ANA

County of ORANGE, California

Brief Legal Description CENTERLINE INTERSECTION OF GUNTHER STREET AND  
WASHINGTON AVENUE

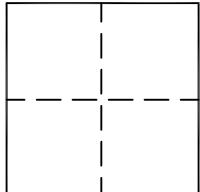

## CORNER TYPE

- Government Corner       Control
- Meander       Property
- Rancho       Other

## COORDINATES (Optional )

N. \_\_\_\_\_ E. \_\_\_\_\_  
 Elevation \_\_\_\_\_  
 Units \_\_\_\_\_ Metric \_\_\_\_\_ U.S. Survey Foot \_\_\_\_\_  
 Horizontal Datum \_\_\_\_\_  
 Zone \_\_\_\_\_ Epoch Date \_\_\_\_\_  
 Vertical Datum \_\_\_\_\_

Date of Survey JULY 18, 2018

- Complies with Public Resources Code §§8801-8819
- Complies with Public Resources Code §§8890-8902

PLS Act Ref:  8765(d)       8771       8773       Other:

Corner/ Monument:	<input checked="" type="checkbox"/> Left as found	<input type="checkbox"/> Established	<input type="checkbox"/> Rebuilt	<input checked="" type="checkbox"/> Pre-Construction
	<input type="checkbox"/> Found and tagged	<input type="checkbox"/> Reestablished	<input type="checkbox"/> Referenced	<input type="checkbox"/> Post-Construction

Narrative of corner identified and monument as found, set, reset, replaced, or removed:

See sheet #2 for description (s):

*THESE TIES ARE FOR THE PURPOSE OF PERPETUATING THE FOUND MONUMENTATION. NO CLAIM IS MADE AS TO THE RELATIONSHIP OF THE POINTS OR LINES SHOWN HEREON TO THE TRUE BOUNDARY LOCATIONS.*

## SURVEYOR'S STATEMENT

This Corner Record was prepared by me or under my direction in conformance with  
the Professional Land Surveyors' Act on SEPTEMBER 17, 2019

Signed Jeffrey J. Lenherr P.L.S. or R.C.E. No. 9305



## COUNTY SURVEYOR'S STATEMENT

This Corner Record was received FEB 4 2019


and examined and filed SEP 27 2019

Signed Kevin R. Hills P.L.S. or R.C.E. No. 6617

Title COUNTY SURVEYOR



County Surveyor's Comment \_\_\_\_\_  
 \_\_\_\_\_  
 \_\_\_\_\_

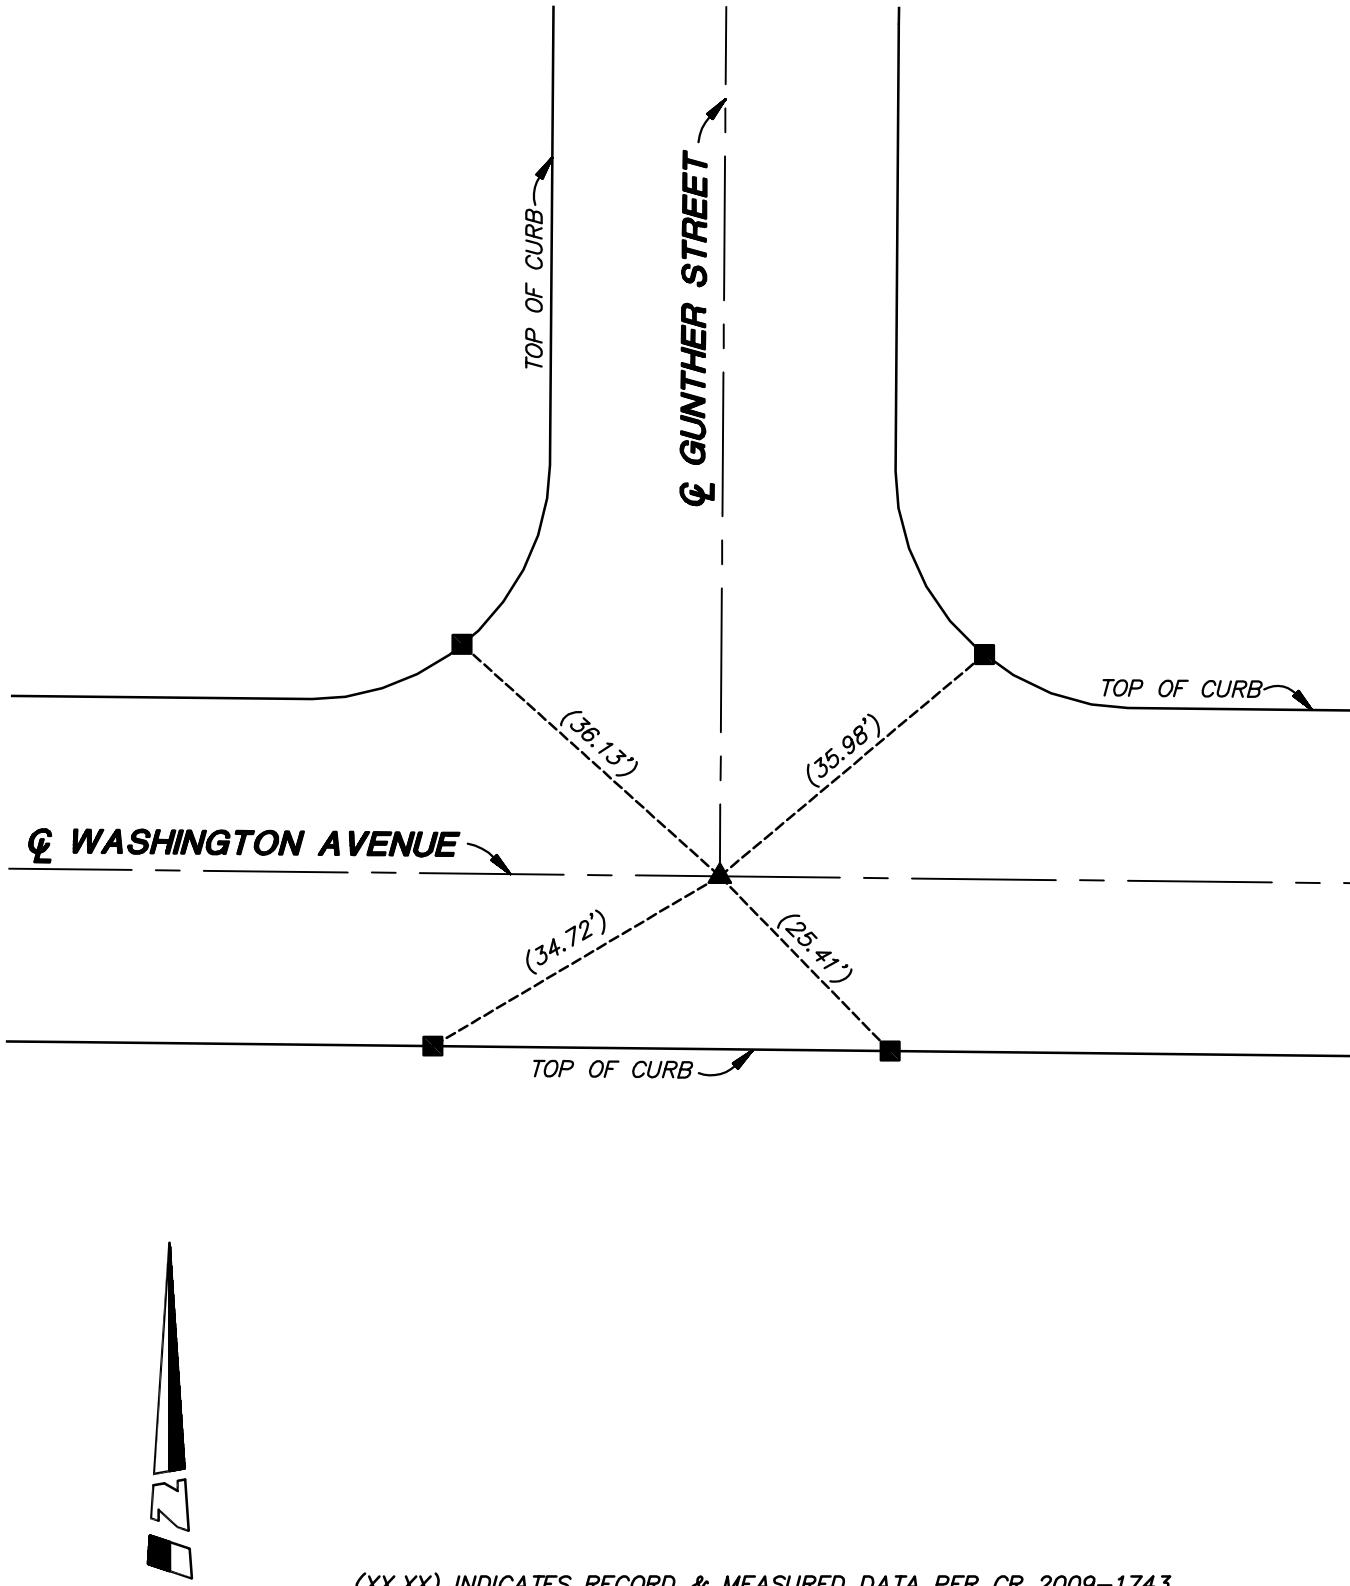

(XX.XX) INDICATES RECORD & MEASURED DATA PER CR 2009-1743

SCALE: 1"=20'

NOTE: THESE TIES ARE FOR THE PURPOSE  
OF PERPETUATING THE FOUND  
MONUMENTATION. NO CLAIM IS MADE AS TO  
THE RELATIONSHIP OF THE POINTS OR LINES  
SHOWN HEREON TO THE TRUE BOUNDARY  
LOCATIONS.

### MONUMENT NOTES

- FOUND CHISELED "X" ON TOP OF CURB PER CR 2009-1743,  
SET LEAD, TACK & TAG "PLS 9305 TIE"
- ▲ FOUND GEAR SPIKE AND WASHER, STAMPED "SANTA ANA  
SURVEY" PER CR 2009-1743, FLUSH

# CORNER RECORD


City of SANTA ANA

Agency Index

Document Number

2019-0582

Brief Legal Description CENTERLINE INTERSECTION OF BEWLEY STREET AND  
WASHINGTON AVENUE

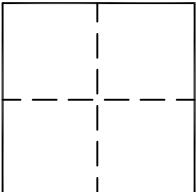

## CORNER TYPE

- Government Corner       Control
- Meander       Property
- Rancho       Other

## COORDINATES (Optional )

N. \_\_\_\_\_ E. \_\_\_\_\_  
 Elevation \_\_\_\_\_  
 Units \_\_\_\_\_ Metric \_\_\_\_\_ U.S. Survey Foot \_\_\_\_\_  
 Horizontal Datum \_\_\_\_\_  
 Zone \_\_\_\_\_ Epoch Date \_\_\_\_\_  
 Vertical Datum \_\_\_\_\_

Date of Survey JULY 18, 2018

- Complies with Public Resources Code §§8801-8819
- Complies with Public Resources Code §§8890-8902

PLS Act Ref:  8765(d)       8771       8773       Other:

Corner/ Monument:	<input checked="" type="checkbox"/> Left as found	<input type="checkbox"/> Established	<input type="checkbox"/> Rebuilt	<input checked="" type="checkbox"/> Pre-Construction
	<input type="checkbox"/> Found and tagged	<input type="checkbox"/> Reestablished	<input type="checkbox"/> Referenced	<input type="checkbox"/> Post-Construction

Narrative of corner identified and monument as found, set, reset, replaced, or removed:

See sheet #2 for description (s):

*THESE TIES ARE FOR THE PURPOSE OF PERPETUATING THE FOUND MONUMENTATION. NO CLAIM IS MADE AS TO THE RELATIONSHIP OF THE POINTS OR LINES SHOWN HEREON TO THE TRUE BOUNDARY LOCATIONS.*

## SURVEYOR'S STATEMENT

This Corner Record was prepared by me or under my direction in conformance with  
the Professional Land Surveyors' Act on SEPTEMBER 17, 2019

Signed Jeffrey J. Lenherr P.L.S. or R.C.E. No. 9305



## COUNTY SURVEYOR'S STATEMENT

This Corner Record was received FEB 4 2019


and examined and filed SEP 27 2019

Signed Kevin R. Hills P.L.S. or R.C.E. No. 6617

Title COUNTY SURVEYOR



County Surveyor's Comment \_\_\_\_\_  
 \_\_\_\_\_  
 \_\_\_\_\_

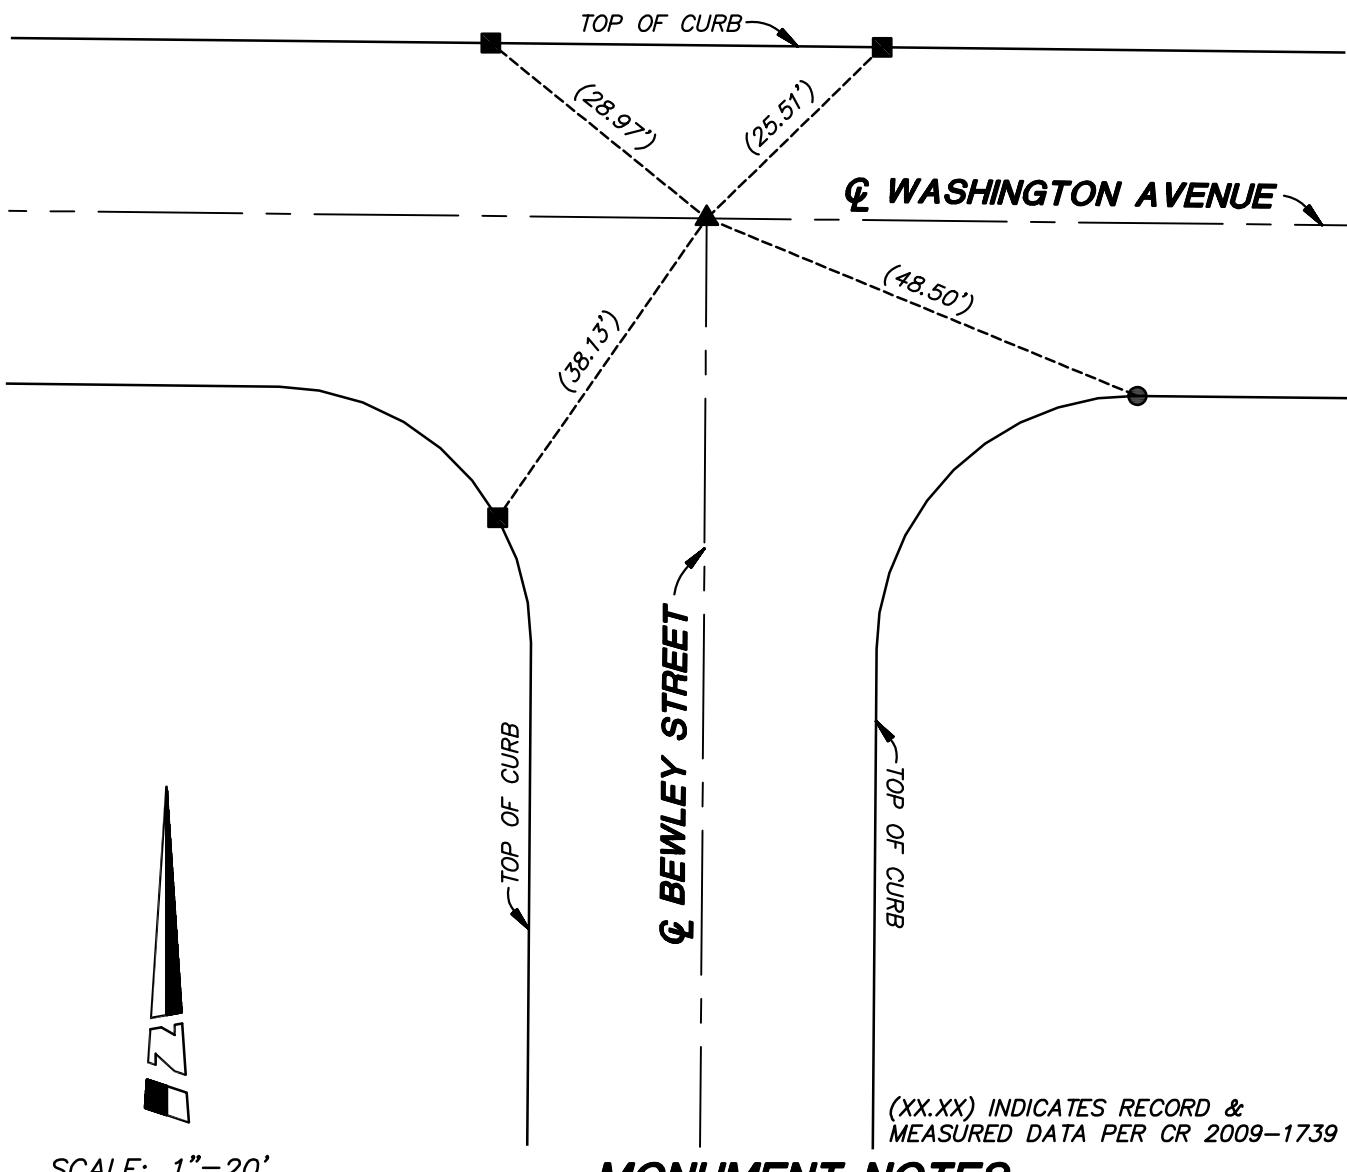

NOTE: THESE TIES ARE FOR THE PURPOSE  
OF PERPETUATING THE FOUND  
MONUMENTATION. NO CLAIM IS MADE AS TO  
THE RELATIONSHIP OF THE POINTS OR LINES  
SHOWN HEREON TO THE TRUE BOUNDARY  
LOCATIONS.

### MONUMENT NOTES

- FOUND CHISELED "X" ON TOP OF CURB PER CR 2009-1739,  
SET LEAD TACK & TAG "PLS 9305 TIE"
- FOUND LEAD, TACK, & CSA TAG ON TOP OF CURB PER CR  
2009-1739
- ▲ FOUND MAG NAIL PER CR 2009-1739, FLUSH

# CORNER RECORD

Agency Index


Document Number

2019-0583

City of SANTA ANA

County of ORANGE, California

Brief Legal Description CENTERLINE INTERSECTION OF BEWLEY STREET AND  
WASHINGTON AVENUE

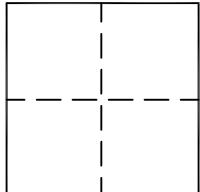

## CORNER TYPE

- Government Corner       Control
- Meander       Property
- Rancho       Other

## COORDINATES (Optional )

N. \_\_\_\_\_ E. \_\_\_\_\_  
 Elevation \_\_\_\_\_  
 Units \_\_\_\_\_ Metric \_\_\_\_\_ U.S. Survey Foot \_\_\_\_\_  
 Horizontal Datum \_\_\_\_\_  
 Zone \_\_\_\_\_ Epoch Date \_\_\_\_\_  
 Vertical Datum \_\_\_\_\_

Date of Survey JULY 18, 2018

- Complies with Public Resources Code §§8801-8819
- Complies with Public Resources Code §§8890-8902

PLS Act Ref:  8765(d)       8771       8773       Other:

Corner/ Monument:	<input checked="" type="checkbox"/> Left as found	<input type="checkbox"/> Established	<input type="checkbox"/> Rebuilt	<input checked="" type="checkbox"/> Pre-Construction
	<input type="checkbox"/> Found and tagged	<input type="checkbox"/> Reestablished	<input type="checkbox"/> Referenced	<input type="checkbox"/> Post-Construction

Narrative of corner identified and monument as found, set, reset, replaced, or removed:

See sheet #2 for description (s):

*THESE TIES ARE FOR THE PURPOSE OF PERPETUATING THE FOUND MONUMENTATION. NO CLAIM IS MADE AS TO THE RELATIONSHIP OF THE POINTS OR LINES SHOWN HEREON TO THE TRUE BOUNDARY LOCATIONS.*

## SURVEYOR'S STATEMENT

This Corner Record was prepared by me or under my direction in conformance with  
the Professional Land Surveyors' Act on SEPTEMBER 17, 2019

Signed Jeffrey J. Lenherr P.L.S. or R.C.E. No. 9305



## COUNTY SURVEYOR'S STATEMENT

This Corner Record was received FEB 4 2019


and examined and filed SEP 27 2019

Signed Kevin R. Hills P.L.S. or R.C.E. No. 6617

Title COUNTY SURVEYOR



County Surveyor's Comment \_\_\_\_\_  
 \_\_\_\_\_  
 \_\_\_\_\_

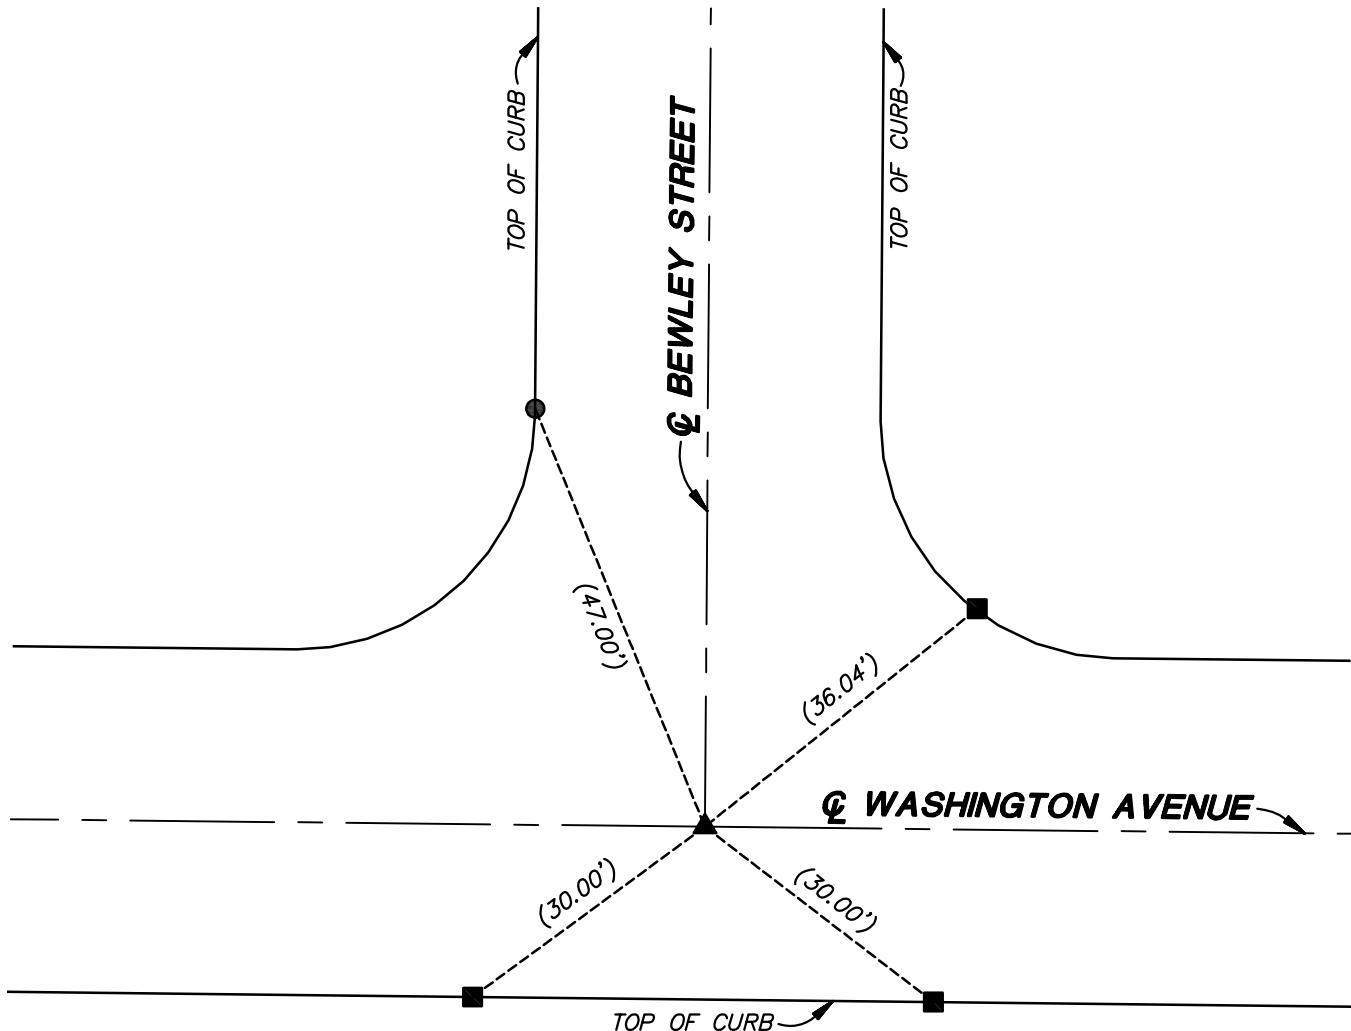

SCALE: 1"=20'

(xx.xx) INDICATES RECORD &amp; MEASURED DATA PER CR 2009-1740

**MONUMENT NOTES**

NOTE: THESE TIES ARE FOR THE PURPOSE OF PERPETUATING THE FOUND MONUMENTATION. NO CLAIM IS MADE AS TO THE RELATIONSHIP OF THE POINTS OR LINES SHOWN HEREON TO THE TRUE BOUNDARY LOCATIONS.

- FOUND CHISELED "X" ON TOP OF CURB PER CR 2009-1740, SET LEAD, TACK & TAG "PLS 9305"
- FOUND LEAD, TACK & CSA TAG ON TOP OF CURB PER CR 2009-1740
- ▲ FOUND PK NAIL, NO REFERENCE, FIT TIES PER CR 2009-1740

# CORNER RECORD

Agency Index


Document Number

2019-0584

City of SANTA ANA

County of ORANGE, California

Brief Legal Description CENTERLINE INTERSECTION OF GUNTHER STREET AND  
MORNINGSIDE AVENUE

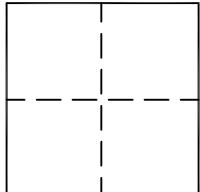

## CORNER TYPE

- Government Corner       Control
- Meander       Property
- Rancho       Other

## COORDINATES (Optional )

N. \_\_\_\_\_ E. \_\_\_\_\_  
 Elevation \_\_\_\_\_  
 Units \_\_\_\_\_ Metric \_\_\_\_\_ U.S. Survey Foot \_\_\_\_\_  
 Horizontal Datum \_\_\_\_\_  
 Zone \_\_\_\_\_ Epoch Date \_\_\_\_\_  
 Vertical Datum \_\_\_\_\_

Date of Survey JULY 18, 2018

- Complies with Public Resources Code §§8801-8819
- Complies with Public Resources Code §§8890-8902

PLS Act Ref:  8765(d)       8771       8773       Other:

Corner/ Monument:	<input checked="" type="checkbox"/> Left as found	<input type="checkbox"/> Established	<input type="checkbox"/> Rebuilt	<input checked="" type="checkbox"/> Pre-Construction
	<input type="checkbox"/> Found and tagged	<input type="checkbox"/> Reestablished	<input type="checkbox"/> Referenced	<input type="checkbox"/> Post-Construction

Narrative of corner identified and monument as found, set, reset, replaced, or removed:

See sheet #2 for description (s):

*THESE TIES ARE FOR THE PURPOSE OF PERPETUATING THE FOUND MONUMENTATION. NO CLAIM IS MADE AS TO THE RELATIONSHIP OF THE POINTS OR LINES SHOWN HEREON TO THE TRUE BOUNDARY LOCATIONS.*

## SURVEYOR'S STATEMENT

This Corner Record was prepared by me or under my direction in conformance with  
the Professional Land Surveyors' Act on SEPTEMBER 17, 2019

Signed Jeffrey J. Lenherr P.L.S. or R.C.E. No. 9305



## COUNTY SURVEYOR'S STATEMENT

This Corner Record was received FEB 4 2019


and examined and filed SEP 27 2019

Signed Kevin R. Hills P.L.S. or R.C.E. No. 6617

Title COUNTY SURVEYOR



County Surveyor's Comment \_\_\_\_\_  
 \_\_\_\_\_  
 \_\_\_\_\_

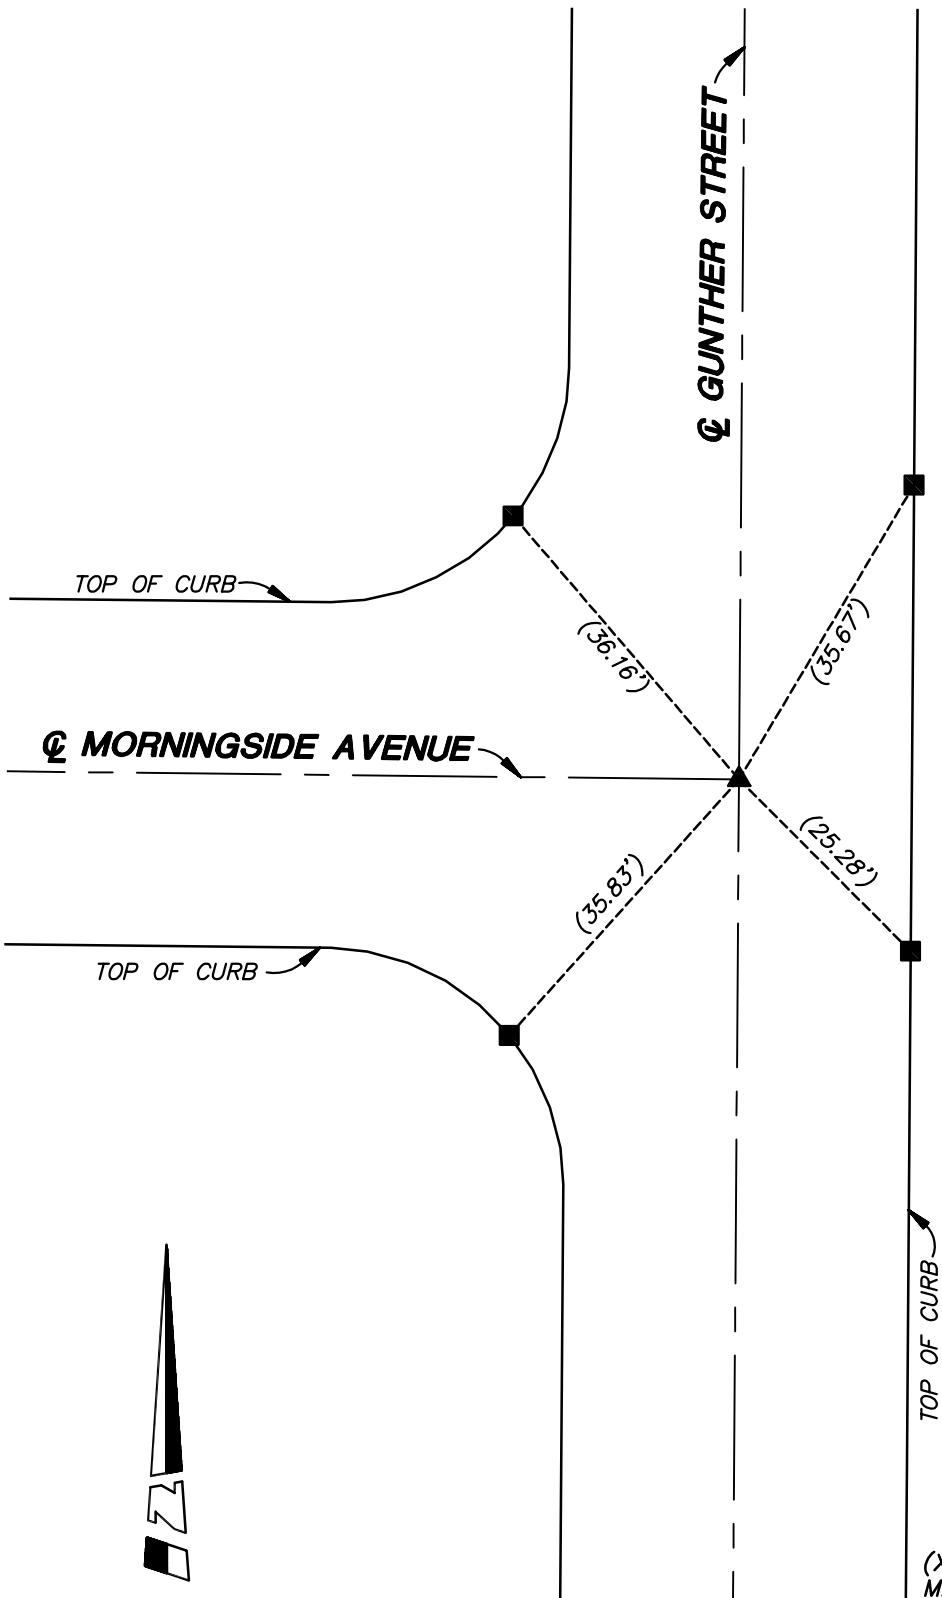

(XX.XX) INDICATES RECORD & MEASURED DATA PER CR 2009-1791

SCALE: 1"=20'

NOTE: THESE TIES ARE FOR THE PURPOSE OF PERPETUATING THE FOUND MONUMENTATION. NO CLAIM IS MADE AS TO THE RELATIONSHIP OF THE POINTS OR LINES SHOWN HEREON TO THE TRUE BOUNDARY LOCATIONS.

### MONUMENT NOTES

- FOUND CHISELED "X" ON TOP OF CURB PER CR 2009-1791, SET LEAD, TACK & TAG "PLS 9305"
- ▲ FOUND GEAR SPIKE AND WASHER, STAMPED "SANTA ANA SURVEY" PER CR 2009-1791

# CORNER RECORD

Agency Index


Document Number

2019-0585

City of SANTA ANA

County of ORANGE, California

Brief Legal Description CENTERLINE CUL-DE-SAC OF MORNINGSIDE AVENUE WESTERLY OF GUNTHER STREET

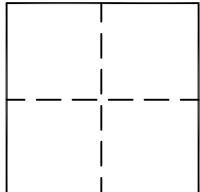

## CORNER TYPE

- Government Corner       Control
- Meander       Property
- Rancho       Other

## COORDINATES (Optional )

N. \_\_\_\_\_ E. \_\_\_\_\_  
 Elevation \_\_\_\_\_  
 Units \_\_\_\_\_ Metric \_\_\_\_\_ U.S. Survey Foot \_\_\_\_\_  
 Horizontal Datum \_\_\_\_\_  
 Zone \_\_\_\_\_ Epoch Date \_\_\_\_\_  
 Vertical Datum \_\_\_\_\_

Date of Survey JULY 18, 2018

- Complies with Public Resources Code §§8801-8819
- Complies with Public Resources Code §§8890-8902

PLS Act Ref:  8765(d)       8771       8773       Other:

Corner/ Monument:	<input checked="" type="checkbox"/> Left as found	<input type="checkbox"/> Established	<input type="checkbox"/> Rebuilt	<input checked="" type="checkbox"/> Pre-Construction
	<input type="checkbox"/> Found and tagged	<input type="checkbox"/> Reestablished	<input type="checkbox"/> Referenced	<input type="checkbox"/> Post-Construction

Narrative of corner identified and monument as found, set, reset, replaced, or removed:

See sheet #2 for description (s):

*THESE TIES ARE FOR THE PURPOSE OF PERPETUATING THE FOUND MONUMENTATION. NO CLAIM IS MADE AS TO THE RELATIONSHIP OF THE POINTS OR LINES SHOWN HEREON TO THE TRUE BOUNDARY LOCATIONS.*

## SURVEYOR'S STATEMENT

This Corner Record was prepared by me or under my direction in conformance with  
the Professional Land Surveyors' Act on SEPTEMBER 17, 2019

Signed Jeffrey J. Lenherr P.L.S. or R.C.E. No. 9305



## COUNTY SURVEYOR'S STATEMENT

This Corner Record was received FEB 4 2019


and examined and filed SEP 27 2019

Signed Kevin R. Hills P.L.S. or R.C.E. No. 6617

Title COUNTY SURVEYOR



County Surveyor's Comment \_\_\_\_\_  
 \_\_\_\_\_  
 \_\_\_\_\_

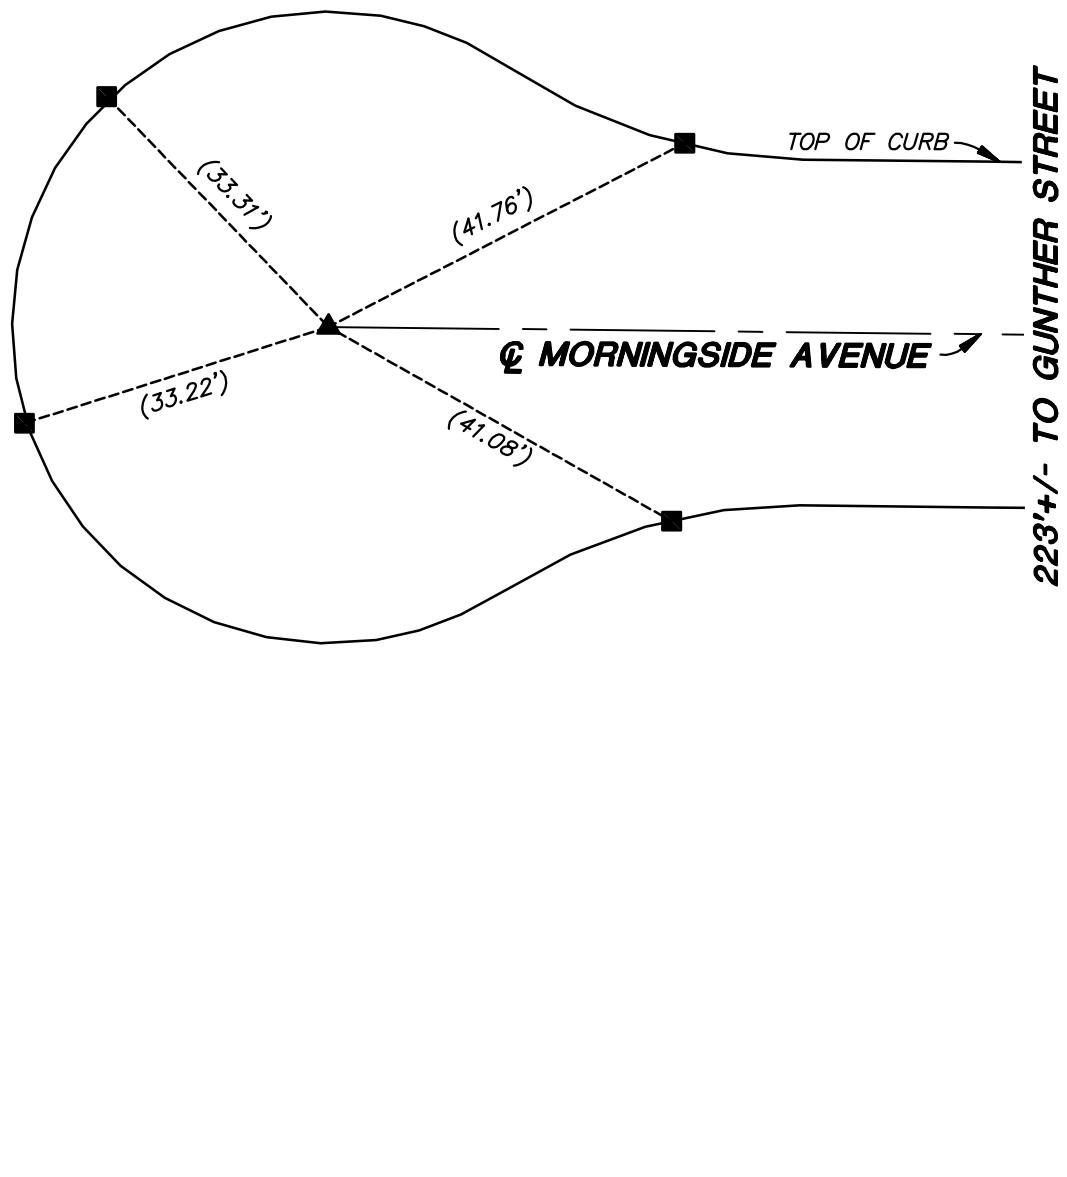

SCALE: 1"=20'

(XX.XX) INDICATES RECORD &amp; MEASURED DATA PER CR 2009-1790

**MONUMENT NOTES**

NOTE: THESE TIES ARE FOR THE PURPOSE  
OF PERPETUATING THE FOUND  
MONUMENTATION. NO CLAIM IS MADE AS TO  
THE RELATIONSHIP OF THE POINTS OR LINES  
SHOWN HEREON TO THE TRUE BOUNDARY  
LOCATIONS.

- FOUND CHISELED "X" ON TOP OF CURB PER CR 2009-1790,  
SET LEAD, TACK & TAG "PLS 9305"
- ▲ FOUND NAIL & TAG, STAMPED "SANTA ANA SURVEY",  
FLUSH PER CR 2009-1790

# CORNER RECORD

Agency Index


Document Number

2019-0586

City of SANTA ANA

County of ORANGE, California

Brief Legal Description CENTERLINE INTERSECTION OF GUNTHER STREET AND SUNSWEPT AVENUE

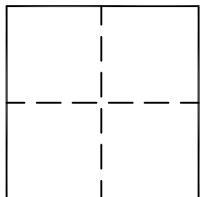

## CORNER TYPE

- Government Corner       Control
- Meander       Property
- Rancho       Other

## COORDINATES (Optional )

N. \_\_\_\_\_ E. \_\_\_\_\_  
 Elevation \_\_\_\_\_  
 Units \_\_\_\_\_ Metric \_\_\_\_\_ U.S. Survey Foot \_\_\_\_\_  
 Horizontal Datum \_\_\_\_\_  
 Zone \_\_\_\_\_ Epoch Date \_\_\_\_\_  
 Vertical Datum \_\_\_\_\_

Date of Survey JULY 18, 2018

- Complies with Public Resources Code §§8801-8819
- Complies with Public Resources Code §§8890-8902

PLS Act Ref:  8765(d)       8771       8773       Other:

Corner/ Monument:	<input checked="" type="checkbox"/> Left as found	<input type="checkbox"/> Established	<input type="checkbox"/> Rebuilt	<input checked="" type="checkbox"/> Pre-Construction
	<input type="checkbox"/> Found and tagged	<input type="checkbox"/> Reestablished	<input type="checkbox"/> Referenced	<input type="checkbox"/> Post-Construction

Narrative of corner identified and monument as found, set, reset, replaced, or removed:

See sheet #2 for description (s):

*THESE TIES ARE FOR THE PURPOSE OF PERPETUATING THE FOUND MONUMENTATION. NO CLAIM IS MADE AS TO THE RELATIONSHIP OF THE POINTS OR LINES SHOWN HEREON TO THE TRUE BOUNDARY LOCATIONS.*

## SURVEYOR'S STATEMENT

This Corner Record was prepared by me or under my direction in conformance with  
the Professional Land Surveyors' Act on SEPTEMBER 17, 2019

Signed Jeffrey J. Lenherr P.L.S. or R.C.E. No. 9305



## COUNTY SURVEYOR'S STATEMENT

This Corner Record was received FEB 4 2019


and examined and filed SEP 27 2019

Signed Kevin R. Hills P.L.S. or R.C.E. No. 6617

Title COUNTY SURVEYOR



County Surveyor's Comment \_\_\_\_\_  
 \_\_\_\_\_  
 \_\_\_\_\_

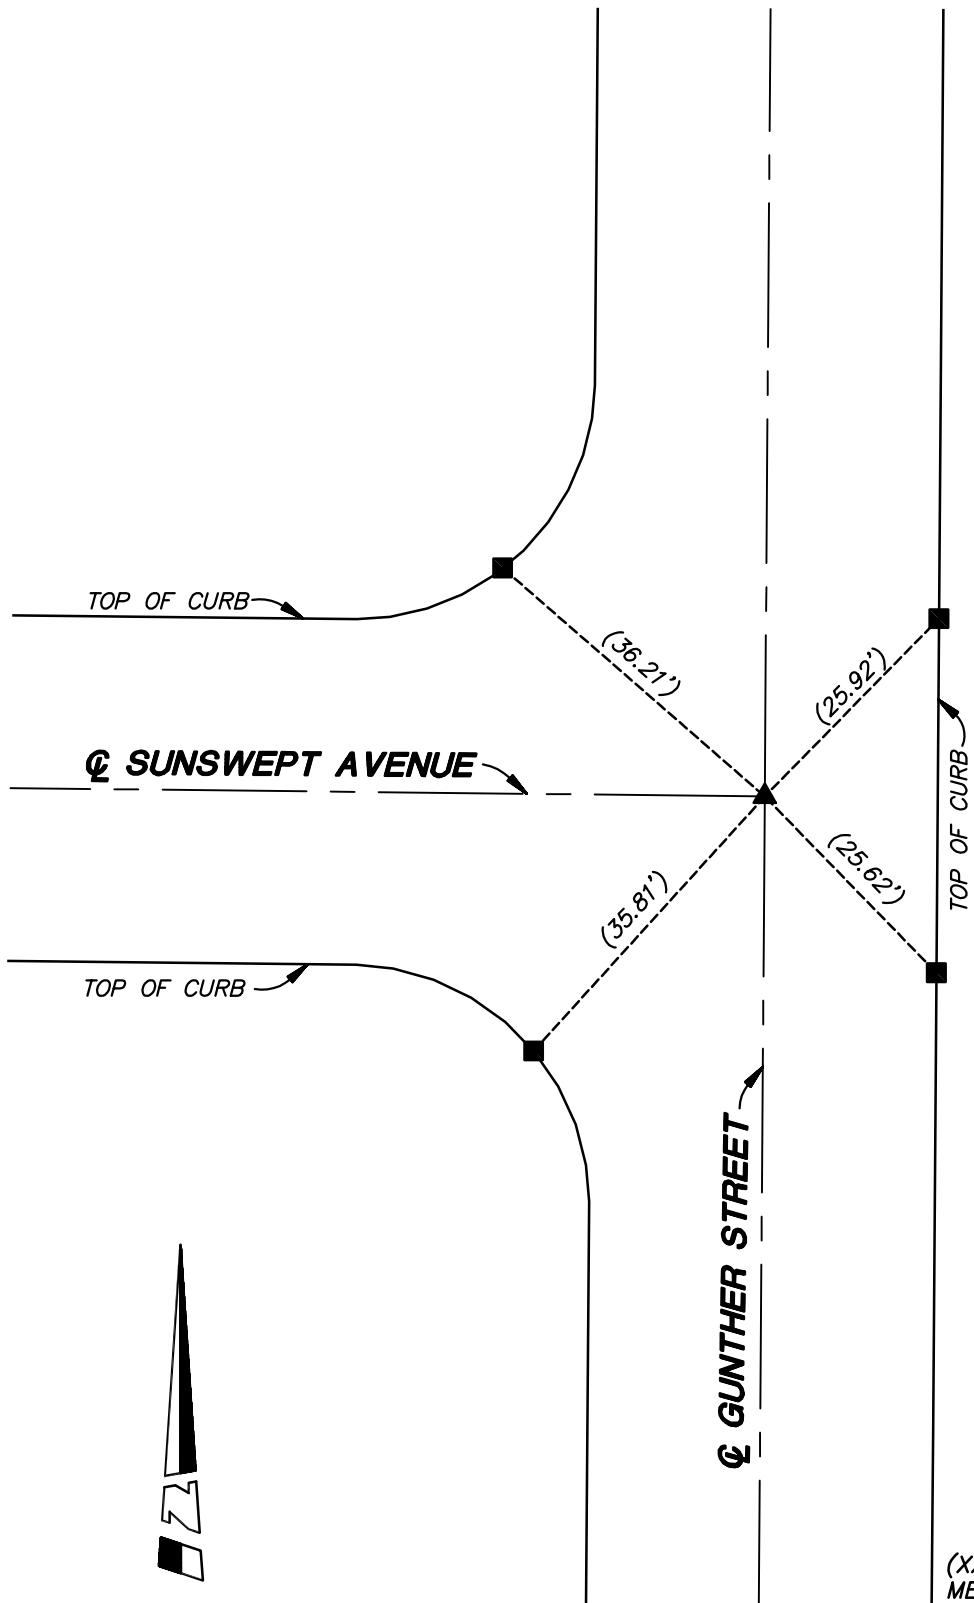

SCALE: 1"=20'

(XX.XX) INDICATES RECORD &  
MEASURED DATA PER CR 2009-1744

NOTE: THESE TIES ARE FOR THE PURPOSE  
OF PERPETUATING THE FOUND  
MONUMENTATION. NO CLAIM IS MADE AS TO  
THE RELATIONSHIP OF THE POINTS OR LINES  
SHOWN HEREON TO THE TRUE BOUNDARY  
LOCATIONS.

### MONUMENT NOTES

- FOUND CHISELED "X" ON TOP OF CURB PER CR 2009-1744,  
SET LEAD, TACK & TAG "PLS 9305 TIE"
- ▲ FOUND SPIKE WITH PUNCH, NO VISIBLE TAG, NO REFERENCE,  
FITS TIES

# CORNER RECORD

Agency Index


Document Number

2019-0587

City of SANTA ANA

County of ORANGE, California

Brief Legal Description CENTERLINE OF SUNSWEPT AVENUE CUL-DE-SAC WESTERLY OF  
GUNTHER STREET

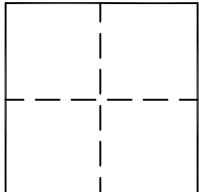

## CORNER TYPE

- Government Corner       Control
- Meander       Property
- Rancho       Other

## COORDINATES (Optional )

N. \_\_\_\_\_ E. \_\_\_\_\_  
 Elevation \_\_\_\_\_  
 Units \_\_\_\_\_ Metric \_\_\_\_\_ U.S. Survey Foot \_\_\_\_\_  
 Horizontal Datum \_\_\_\_\_  
 Zone \_\_\_\_\_ Epoch Date \_\_\_\_\_  
 Vertical Datum \_\_\_\_\_

Date of Survey JULY 18, 2018

- Complies with Public Resources Code §§8801-8819
- Complies with Public Resources Code §§8890-8902

PLS Act Ref:  8765(d)       8771       8773       Other:

Corner/ Monument:	<input checked="" type="checkbox"/> Left as found	<input type="checkbox"/> Established	<input type="checkbox"/> Rebuilt	<input checked="" type="checkbox"/> Pre-Construction
	<input type="checkbox"/> Found and tagged	<input type="checkbox"/> Reestablished	<input type="checkbox"/> Referenced	<input type="checkbox"/> Post-Construction

Narrative of corner identified and monument as found, set, reset, replaced, or removed:

See sheet #2 for description (s):

*THESE TIES ARE FOR THE PURPOSE OF PERPETUATING THE FOUND MONUMENTATION. NO CLAIM IS MADE AS TO THE RELATIONSHIP OF THE POINTS OR LINES SHOWN HEREON TO THE TRUE BOUNDARY LOCATIONS.*

## SURVEYOR'S STATEMENT

This Corner Record was prepared by me or under my direction in conformance with  
the Professional Land Surveyors' Act on SEPTEMBER 17, 2019

Signed Jeffrey J. Lenherr P.L.S. or R.C.E. No. 9305



## COUNTY SURVEYOR'S STATEMENT

This Corner Record was received FEB 4 2019


and examined and filed SEP 27 2019

Signed Kevin R. Hills P.L.S. or R.C.E. No. 6617

Title COUNTY SURVEYOR



County Surveyor's Comment \_\_\_\_\_  
 \_\_\_\_\_  
 \_\_\_\_\_

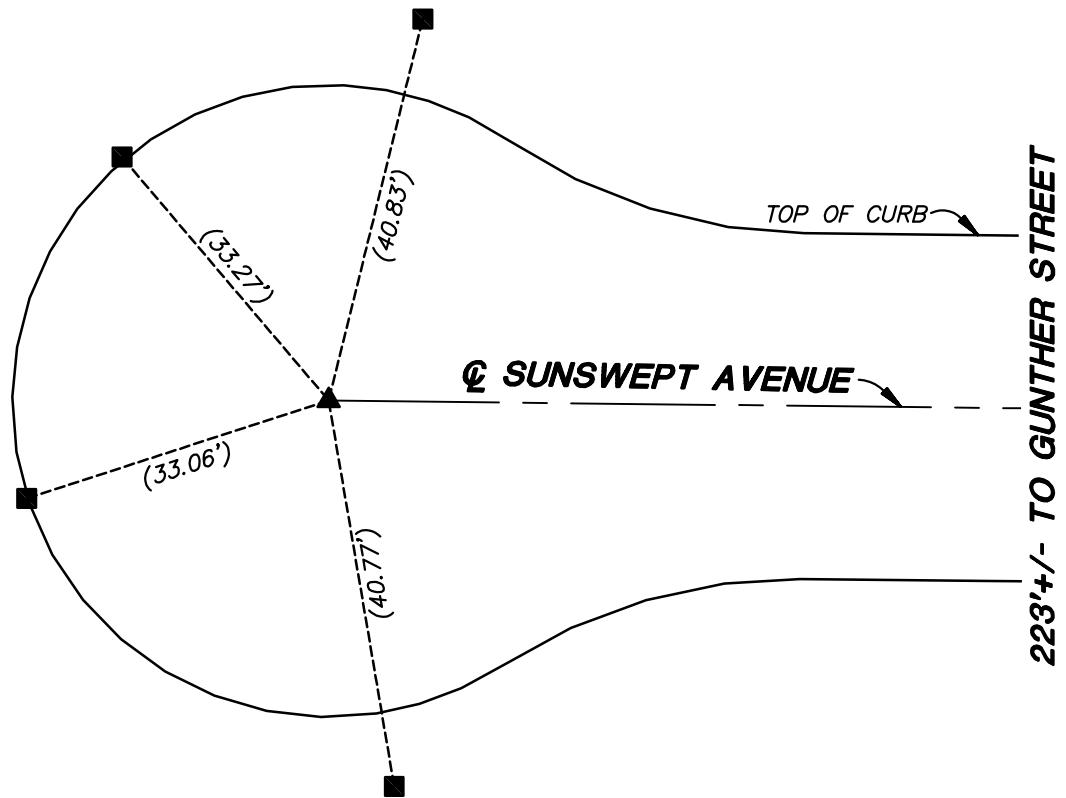

SCALE: 1"=20'

(XX.XX) INDICATES RECORD & MEASURED DATA PER CR 2009-1751

NOTE: THESE TIES ARE FOR THE PURPOSE  
OF PERPETUATING THE FOUND  
MONUMENTATION. NO CLAIM IS MADE AS TO  
THE RELATIONSHIP OF THE POINTS OR LINES  
SHOWN HEREON TO THE TRUE BOUNDARY  
LOCATIONS.

### MONUMENT NOTES

- FOUND CHISELED "X" ON TOP OF CURB PER CR 2009-1751,  
SET LEAD, TACK & TAG "PLS 9305 TIE"
- ▲ FOUND NAIL & TAG, STAMPED "SANTA ANA SURVEY" PER  
CR 2009-1751, FLUSH

# CORNER RECORD

Agency Index


Document Number

2019-0589

City of SANTA ANA

County of ORANGE, California

Brief Legal Description CENTERLINE CURVE OF GUNTHER STREET BETWEEN SUNSWEPT AVENUE AND BOYER AVENUE

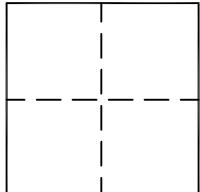

## CORNER TYPE

- Government Corner       Control
- Meander       Property
- Rancho       Other

## COORDINATES (Optional )

N. \_\_\_\_\_ E. \_\_\_\_\_  
 Elevation \_\_\_\_\_  
 Units \_\_\_\_\_ Metric \_\_\_\_\_ U.S. Survey Foot \_\_\_\_\_  
 Horizontal Datum \_\_\_\_\_  
 Zone \_\_\_\_\_ Epoch Date \_\_\_\_\_  
 Vertical Datum \_\_\_\_\_

Date of Survey JULY 18, 2018

- Complies with Public Resources Code §§8801-8819
- Complies with Public Resources Code §§8890-8902

PLS Act Ref:  8765(d)       8771       8773       Other:

Corner/ Monument:	<input checked="" type="checkbox"/> Left as found	<input type="checkbox"/> Established	<input type="checkbox"/> Rebuilt	<input checked="" type="checkbox"/> Pre-Construction
	<input type="checkbox"/> Found and tagged	<input type="checkbox"/> Reestablished	<input type="checkbox"/> Referenced	<input type="checkbox"/> Post-Construction

Narrative of corner identified and monument as found, set, reset, replaced, or removed:

See sheet #2 for description (s):

*THESE TIES ARE FOR THE PURPOSE OF PERPETUATING THE FOUND MONUMENTATION. NO CLAIM IS MADE AS TO THE RELATIONSHIP OF THE POINTS OR LINES SHOWN HEREON TO THE TRUE BOUNDARY LOCATIONS.*

## SURVEYOR'S STATEMENT

This Corner Record was prepared by me or under my direction in conformance with  
the Professional Land Surveyors' Act on SEPTEMBER 17, 2019

Signed Jeffrey J. Lenherr P.L.S. or R.C.E. No. 9305



## COUNTY SURVEYOR'S STATEMENT

This Corner Record was received FEB 4 2019


and examined and filed SEP 27 2019

Signed Kevin R. Hills P.L.S. or R.C.E. No. 6617

Title COUNTY SURVEYOR



County Surveyor's Comment \_\_\_\_\_  
 \_\_\_\_\_  
 \_\_\_\_\_

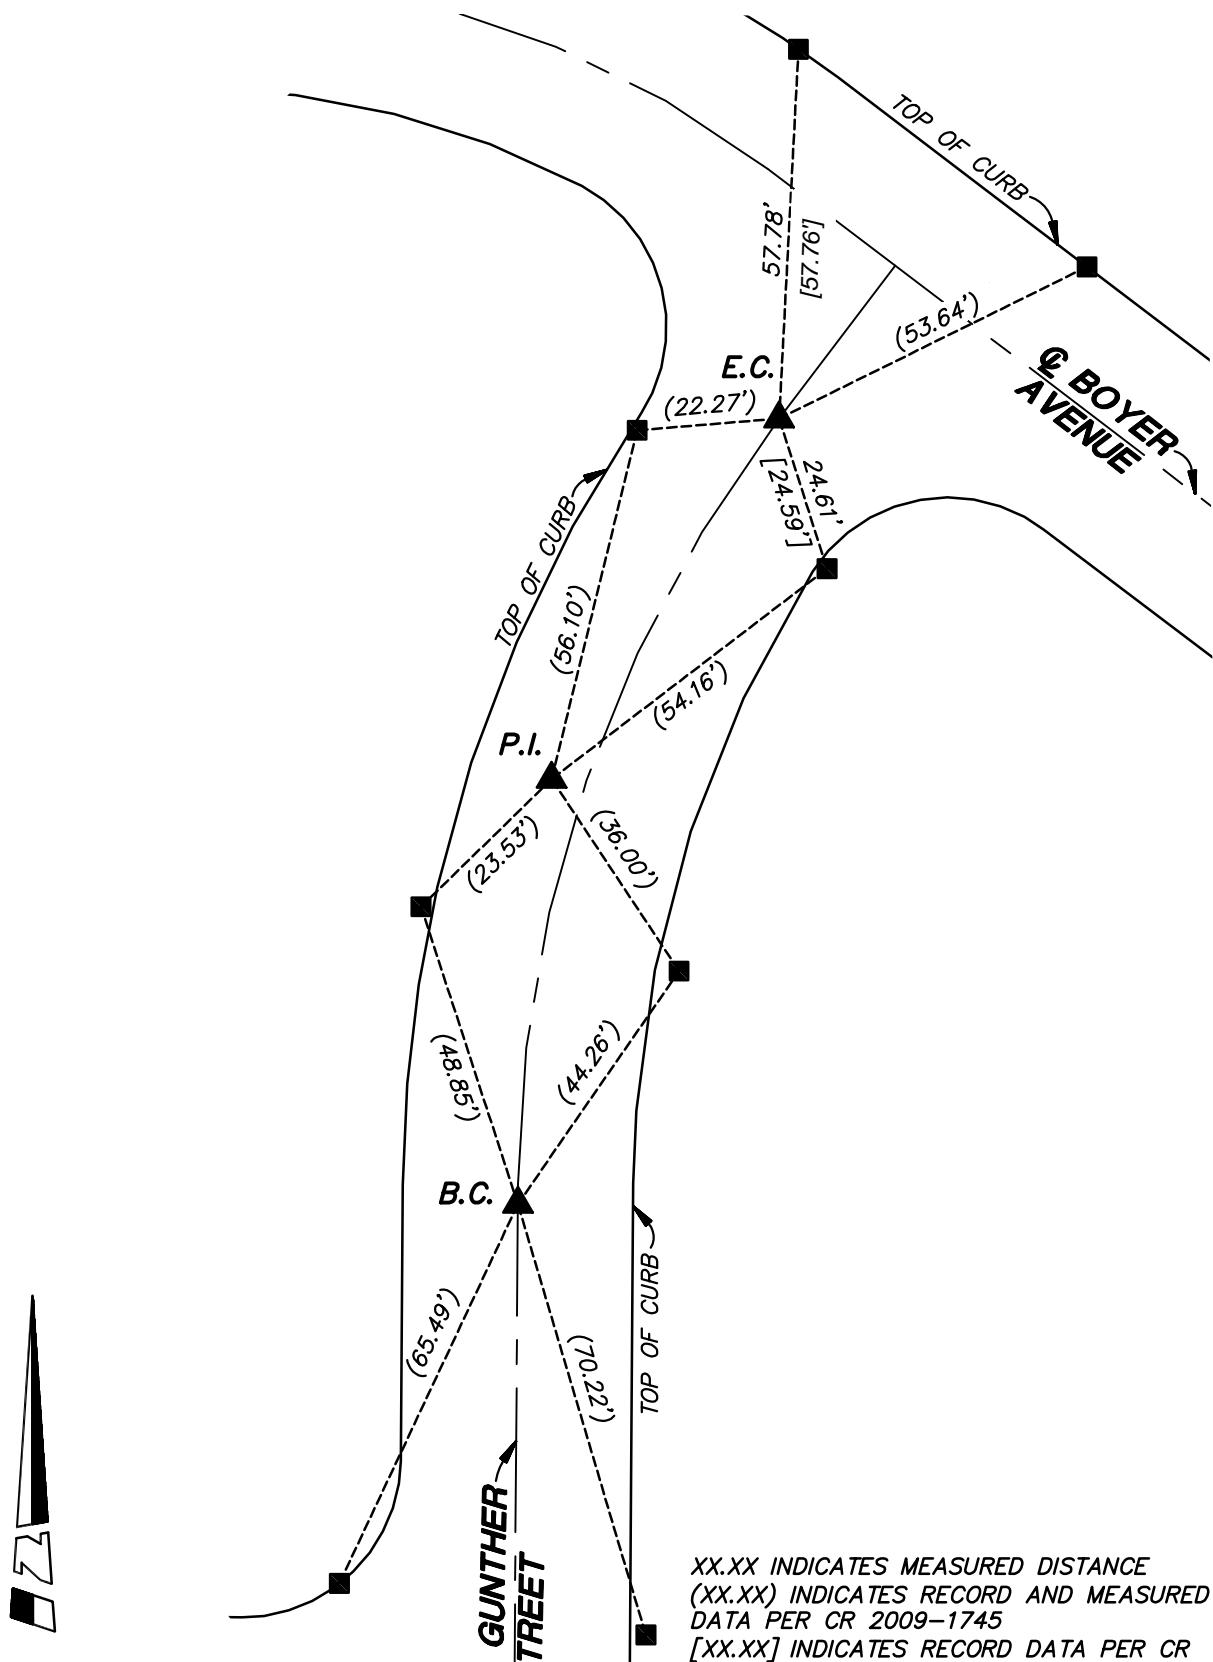

NOTE: THESE TIES ARE FOR THE PURPOSE  
OF PERPETUATING THE FOUND  
MONUMENTATION. NO CLAIM IS MADE AS TO  
THE RELATIONSHIP OF THE POINTS OR LINES  
SHOWN HEREON TO THE TRUE BOUNDARY  
LOCATIONS.

XX.XX INDICATES MEASURED DISTANCE  
(XX.XX) INDICATES RECORD AND MEASURED  
DATA PER CR 2009-1745  
[XX.XX] INDICATES RECORD DATA PER CR  
2009-1745

### MONUMENT NOTES

- FOUND CHISELED "X" ON TOP OF CURB PER CR 2009-1745, SET LEAD, TACK & TAG "PLS 9305 TIE"
- ▲ FOUND NAIL & TAG, STAMPED "SANTA ANA SURVEY" PER CR 2009-1745, FLUSH

# CORNER RECORD

Agency Index


Document Number

2019-0590

City of SANTA ANA

County of ORANGE, California

Brief Legal Description CENTERLINE CUL-DE-SAC OF BEWLEY STREET NORTH OF BOYER AVENUE

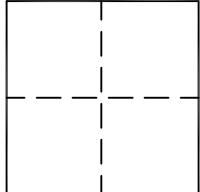

## CORNER TYPE

- Government Corner       Control
- Meander       Property
- Rancho       Other

## COORDINATES (Optional )

N. \_\_\_\_\_ E. \_\_\_\_\_  
 Elevation \_\_\_\_\_  
 Units \_\_\_\_\_ Metric \_\_\_\_\_ U.S. Survey Foot \_\_\_\_\_  
 Horizontal Datum \_\_\_\_\_  
 Zone \_\_\_\_\_ Epoch Date \_\_\_\_\_  
 Vertical Datum \_\_\_\_\_

Date of Survey JULY 18, 2018

- Complies with Public Resources Code §§8801-8819
- Complies with Public Resources Code §§8890-8902

PLS Act Ref:  8765(d)       8771       8773       Other:

Corner/ Monument:	<input checked="" type="checkbox"/> Left as found	<input type="checkbox"/> Established	<input type="checkbox"/> Rebuilt	<input checked="" type="checkbox"/> Pre-Construction
	<input type="checkbox"/> Found and tagged	<input type="checkbox"/> Reestablished	<input type="checkbox"/> Referenced	<input type="checkbox"/> Post-Construction

Narrative of corner identified and monument as found, set, reset, replaced, or removed:

See sheet #2 for description (s):

*THESE TIES ARE FOR THE PURPOSE OF PERPETUATING THE FOUND MONUMENTATION. NO CLAIM IS MADE AS TO THE RELATIONSHIP OF THE POINTS OR LINES SHOWN HEREON TO THE TRUE BOUNDARY LOCATIONS.*

## SURVEYOR'S STATEMENT

This Corner Record was prepared by me or under my direction in conformance with  
the Professional Land Surveyors' Act on SEPTEMBER 17, 2019

Signed Jeffrey J. Lenherr P.L.S. or R.C.E. No. 9305



## COUNTY SURVEYOR'S STATEMENT

This Corner Record was received FEB 4 2019


and examined and filed SEP 27 2019

Signed Kevin R. Hills P.L.S. or R.C.E. No. 6617

Title COUNTY SURVEYOR



County Surveyor's Comment \_\_\_\_\_  
 \_\_\_\_\_  
 \_\_\_\_\_

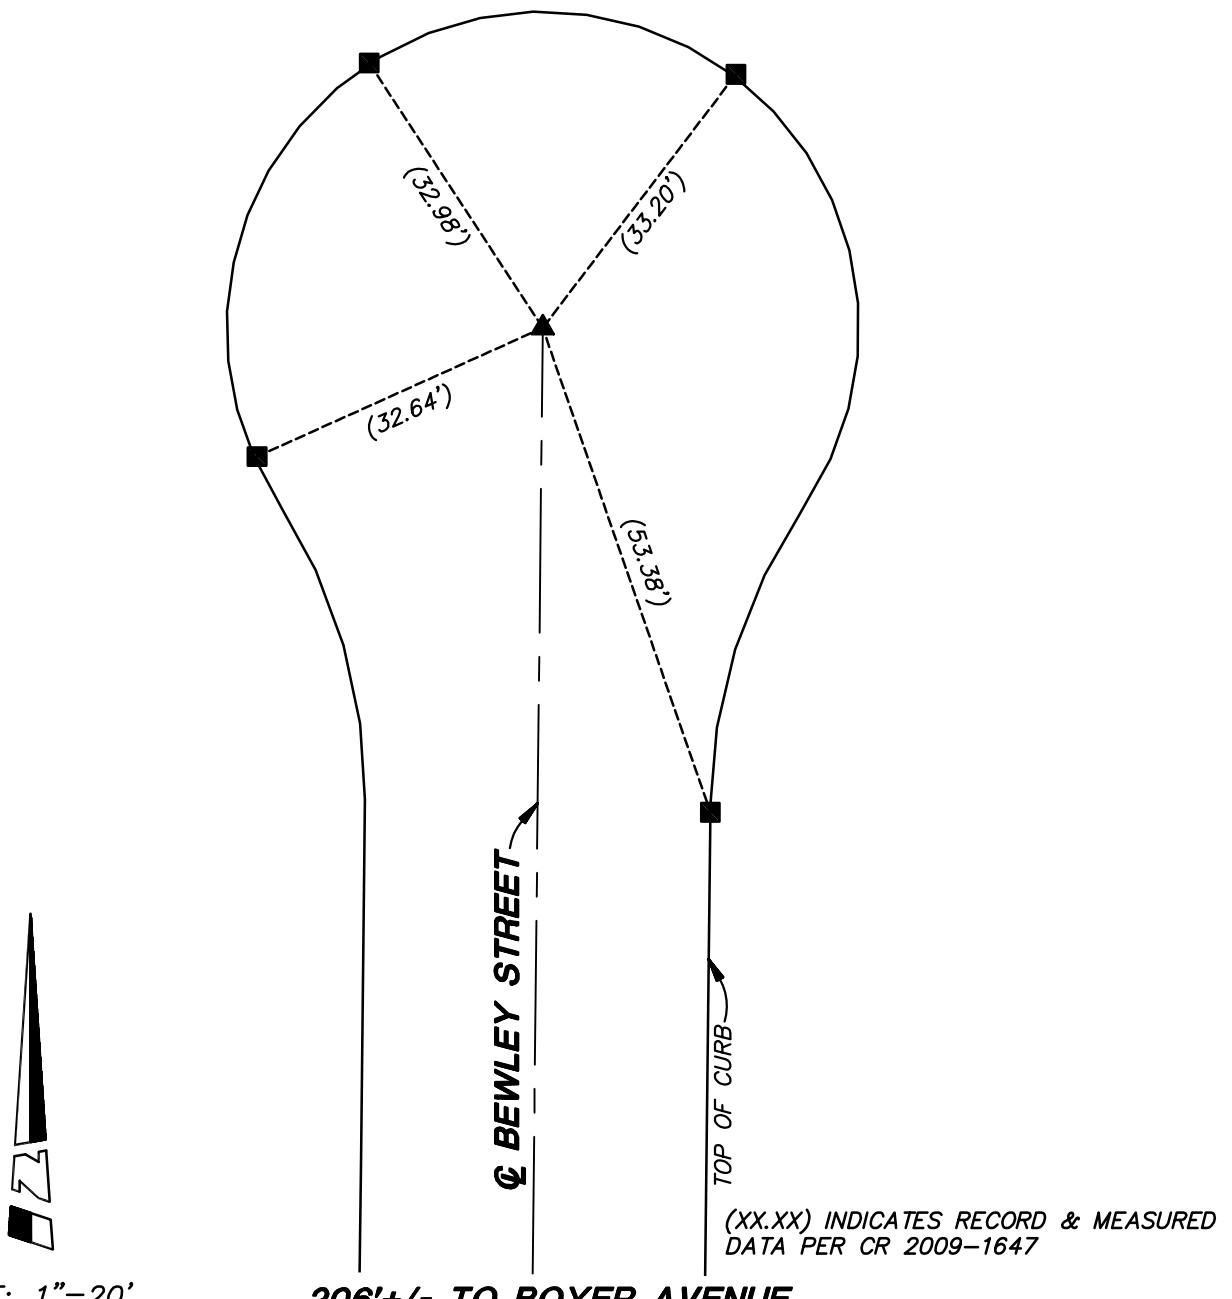

SCALE: 1"=20'

206'+/- TO BOYER AVENUE

**MONUMENT NOTES**

NOTE: THESE TIES ARE FOR THE PURPOSE OF PERPETUATING THE FOUND MONUMENTATION. NO CLAIM IS MADE AS TO THE RELATIONSHIP OF THE POINTS OR LINES SHOWN HEREON TO THE TRUE BOUNDARY LOCATIONS.

- FOUND CHISELED "X" ON TOP OF CURB PER CR 2009-1647, SET LEAD, TACK & TAG "PLS 9305 TIE"
- ▲ FOUND NAIL & TAG, STAMPED "SANTA ANA SURVEY" PER CR 2009-1647, FLUSH

# CORNER RECORD

Agency Index


Document Number

2019-0591

City of SANTA ANA

County of ORANGE, California

Brief Legal Description CENTERLINE INTERSECTION OF BEWLEY STREET AND BOYER AVENUE

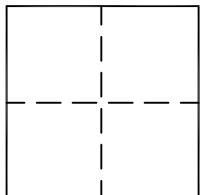

## CORNER TYPE

- Government Corner       Control
- Meander       Property
- Rancho       Other

## COORDINATES (Optional )

N. \_\_\_\_\_ E. \_\_\_\_\_  
 Elevation \_\_\_\_\_  
 Units \_\_\_\_\_ Metric \_\_\_\_\_ U.S. Survey Foot \_\_\_\_\_  
 Horizontal Datum \_\_\_\_\_  
 Zone \_\_\_\_\_ Epoch Date \_\_\_\_\_  
 Vertical Datum \_\_\_\_\_

Date of Survey JULY 18, 2018

- Complies with Public Resources Code §§8801-8819
- Complies with Public Resources Code §§8890-8902

PLS Act Ref:  8765(d)       8771       8773       Other:

Corner/ Monument:	<input checked="" type="checkbox"/> Left as found	<input type="checkbox"/> Established	<input type="checkbox"/> Rebuilt	<input checked="" type="checkbox"/> Pre-Construction
	<input type="checkbox"/> Found and tagged	<input type="checkbox"/> Reestablished	<input type="checkbox"/> Referenced	<input type="checkbox"/> Post-Construction

Narrative of corner identified and monument as found, set, reset, replaced, or removed:

See sheet #2 for description (s):

*THESE TIES ARE FOR THE PURPOSE OF PERPETUATING THE FOUND MONUMENTATION. NO CLAIM IS MADE AS TO THE RELATIONSHIP OF THE POINTS OR LINES SHOWN HEREON TO THE TRUE BOUNDARY LOCATIONS.*

## SURVEYOR'S STATEMENT

This Corner Record was prepared by me or under my direction in conformance with  
the Professional Land Surveyors' Act on SEPTEMBER 17, 2019

Signed Jeffrey J. Lenherr P.L.S. or R.C.E. No. 9305



## COUNTY SURVEYOR'S STATEMENT

This Corner Record was received FEB 4 2019


and examined and filed SEP 27 2019

Signed Kevin R. Hills P.L.S. or R.C.E. No. 6617

Title COUNTY SURVEYOR



County Surveyor's Comment \_\_\_\_\_  
 \_\_\_\_\_  
 \_\_\_\_\_

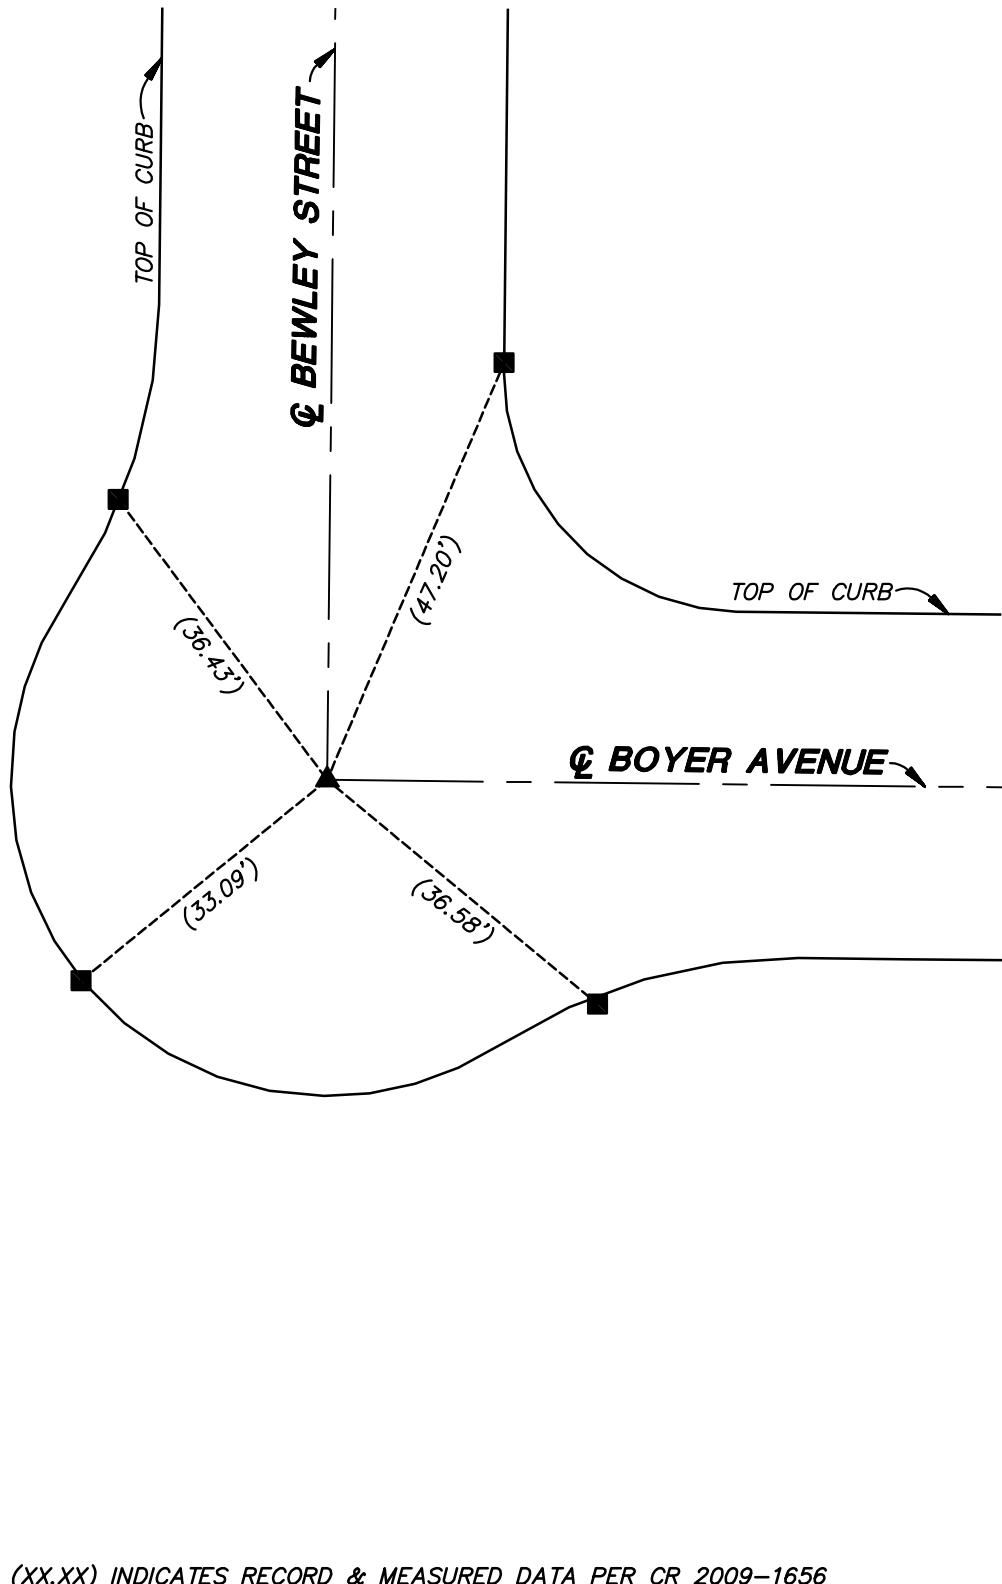

(XX.XX) INDICATES RECORD & MEASURED DATA PER CR 2009-1656

SCALE: 1"=20'

NOTE: THESE TIES ARE FOR THE PURPOSE  
OF PERPETUATING THE FOUND  
MONUMENTATION. NO CLAIM IS MADE AS TO  
THE RELATIONSHIP OF THE POINTS OR LINES  
SHOWN HEREON TO THE TRUE BOUNDARY  
LOCATIONS.

### MONUMENT NOTES

- FOUND CHISELED "X" ON TOP OF CURB PER CR 2009-1656,  
SET LEAD, TACK & TAG "PLS 9305 TIE"
- ▲ FOUND NAIL & TAG, STAMPED "SANTA ANA SURVEY" PER  
CR 2009-1656

# CORNER RECORD

Agency Index


Document Number

2019-0592

City of SANTA ANA

County of ORANGE, California

Brief Legal Description CENTERLINE OF BOYER AVENUE, 1ST CURVE WESTERLY OF GUNTHER STREET

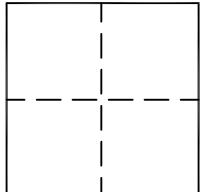

## CORNER TYPE

- Government Corner       Control
- Meander       Property
- Rancho       Other

## COORDINATES (Optional )

N. \_\_\_\_\_ E. \_\_\_\_\_  
 Elevation \_\_\_\_\_  
 Units \_\_\_\_\_ Metric \_\_\_\_\_ U.S. Survey Foot \_\_\_\_\_  
 Horizontal Datum \_\_\_\_\_  
 Zone \_\_\_\_\_ Epoch Date \_\_\_\_\_  
 Vertical Datum \_\_\_\_\_

Date of Survey JULY 18, 2018

- Complies with Public Resources Code §§8801-8819
- Complies with Public Resources Code §§8890-8902

PLS Act Ref:  8765(d)       8771       8773       Other:

Corner/ Monument:	<input checked="" type="checkbox"/> Left as found	<input type="checkbox"/> Established	<input type="checkbox"/> Rebuilt	<input checked="" type="checkbox"/> Pre-Construction
	<input type="checkbox"/> Found and tagged	<input type="checkbox"/> Reestablished	<input type="checkbox"/> Referenced	<input type="checkbox"/> Post-Construction

Narrative of corner identified and monument as found, set, reset, replaced, or removed:

See sheet #2 for description (s):

*THESE TIES ARE FOR THE PURPOSE OF PERPETUATING THE FOUND MONUMENTATION. NO CLAIM IS MADE AS TO THE RELATIONSHIP OF THE POINTS OR LINES SHOWN HEREON TO THE TRUE BOUNDARY LOCATIONS.*

## SURVEYOR'S STATEMENT

This Corner Record was prepared by me or under my direction in conformance with  
the Professional Land Surveyors' Act on SEPTEMBER 17, 2019

Signed Jeffrey J. Lenherr P.L.S. or R.C.E. No. 9305



## COUNTY SURVEYOR'S STATEMENT

This Corner Record was received FEB 4 2019

and examined and filed SEP 27 2019


Signed Kevin R. Hills P.L.S. or R.C.E. No. 6617

Title COUNTY SURVEYOR



County Surveyor's Comment \_\_\_\_\_  
 \_\_\_\_\_  
 \_\_\_\_\_

\* MEASURED DISTANCE VERIFIED BY CHAIN

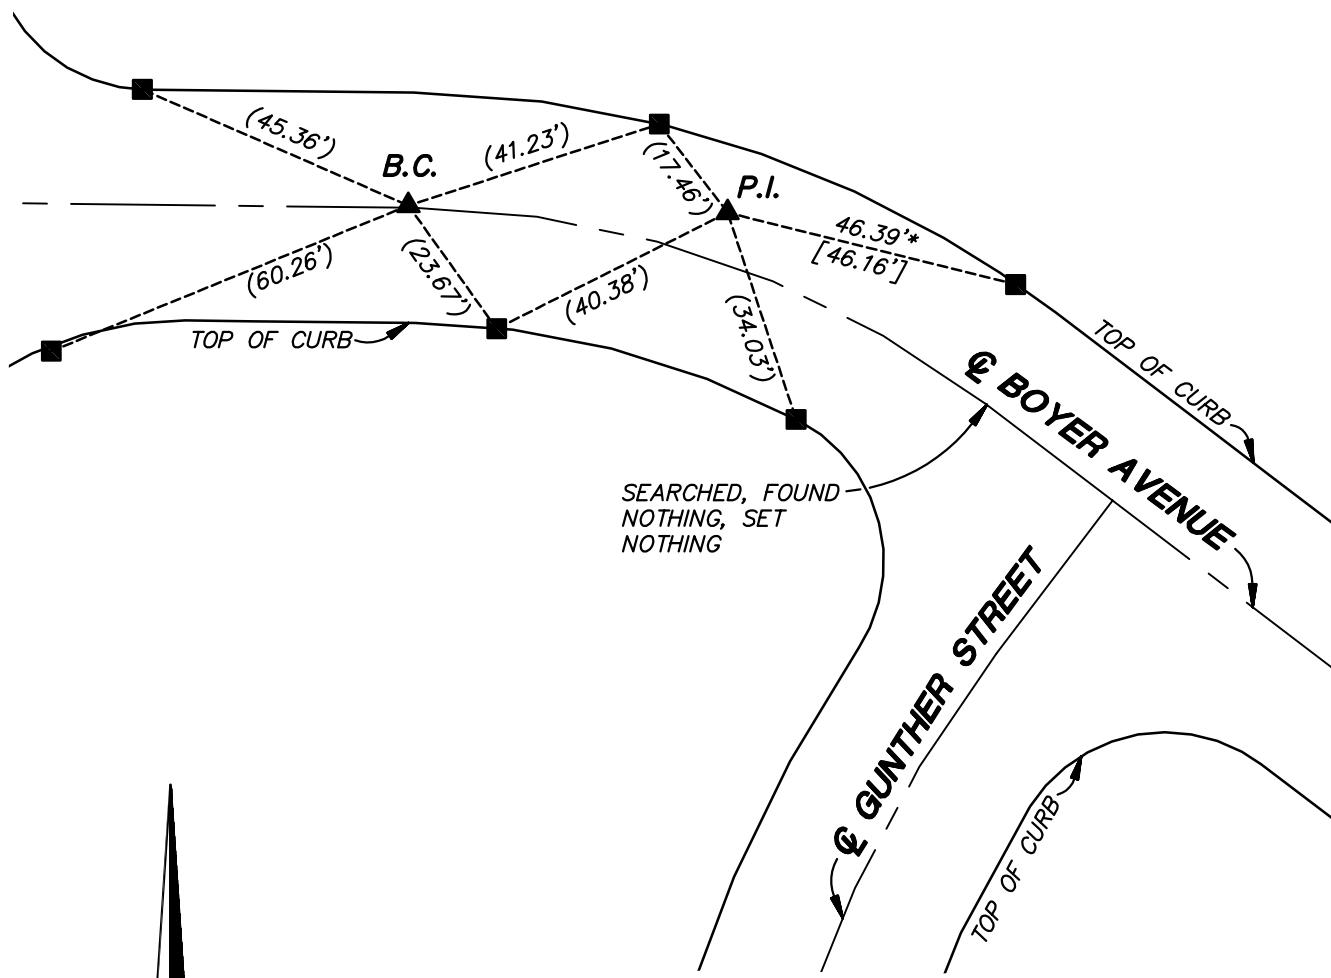

XX.XX INDICATES MEASURED DISTANCE

(XX.XX) INDICATES RECORD & MEASURED DATA PER CR 2009-1750

[XX.XX] INDICATES RECORD DATA PER CR 2009-1750

SCALE: 1"=30'

## MONUMENT NOTES

NOTE: THESE TIES ARE FOR THE PURPOSE OF PERPETUATING THE FOUND MONUMENTATION. NO CLAIM IS MADE AS TO THE RELATIONSHIP OF THE POINTS OR LINES SHOWN HEREON TO THE TRUE BOUNDARY LOCATIONS.

- FOUND CHISELED "X" ON TOP OF CURB PER CR 2009-1750, SET LEAD, TACK & TAG "PLS 9305 TIE"
- ▲ FOUND NAIL & TAG, STAMPED "SANTA ANA SURVEY" PER CR 2009-1750

# CORNER RECORD

Agency Index


Document Number

2019-0593

City of SANTA ANA

County of ORANGE, California

Brief Legal Description CENTERLINE INTERSECTION OF GUNTHER STREET AND BOYER AVENUE

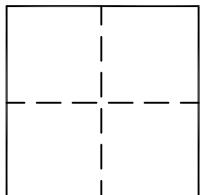

## CORNER TYPE

- Government Corner       Control
- Meander       Property
- Rancho       Other

## COORDINATES (Optional )

N. \_\_\_\_\_ E. \_\_\_\_\_  
 Elevation \_\_\_\_\_  
 Units \_\_\_\_\_ Metric \_\_\_\_\_ U.S. Survey Foot \_\_\_\_\_  
 Horizontal Datum \_\_\_\_\_  
 Zone \_\_\_\_\_ Epoch Date \_\_\_\_\_  
 Vertical Datum \_\_\_\_\_

Date of Survey JULY 18, 2018

- Complies with Public Resources Code §§8801-8819
- Complies with Public Resources Code §§8890-8902

PLS Act Ref:  8765(d)       8771       8773       Other:

Corner/ Monument:	<input checked="" type="checkbox"/> Left as found	<input type="checkbox"/> Established	<input type="checkbox"/> Rebuilt	<input checked="" type="checkbox"/> Pre-Construction
	<input type="checkbox"/> Found and tagged	<input type="checkbox"/> Reestablished	<input type="checkbox"/> Referenced	<input type="checkbox"/> Post-Construction

Narrative of corner identified and monument as found, set, reset, replaced, or removed:

See sheet #2 for description (s):

*THESE TIES ARE FOR THE PURPOSE OF PERPETUATING THE FOUND MONUMENTATION. NO CLAIM IS MADE AS TO THE RELATIONSHIP OF THE POINTS OR LINES SHOWN HEREON TO THE TRUE BOUNDARY LOCATIONS.*

## SURVEYOR'S STATEMENT

This Corner Record was prepared by me or under my direction in conformance with  
the Professional Land Surveyors' Act on SEPTEMBER 17, 2019

Signed Jeffrey J. Lenherr P.L.S. or R.C.E. No. 9305



## COUNTY SURVEYOR'S STATEMENT

This Corner Record was received FEB 4 2019


and examined and filed SEP 27 2019

Signed Kevin R. Hills P.L.S. or R.C.E. No. 6617

Title COUNTY SURVEYOR



County Surveyor's Comment \_\_\_\_\_  
 \_\_\_\_\_  
 \_\_\_\_\_

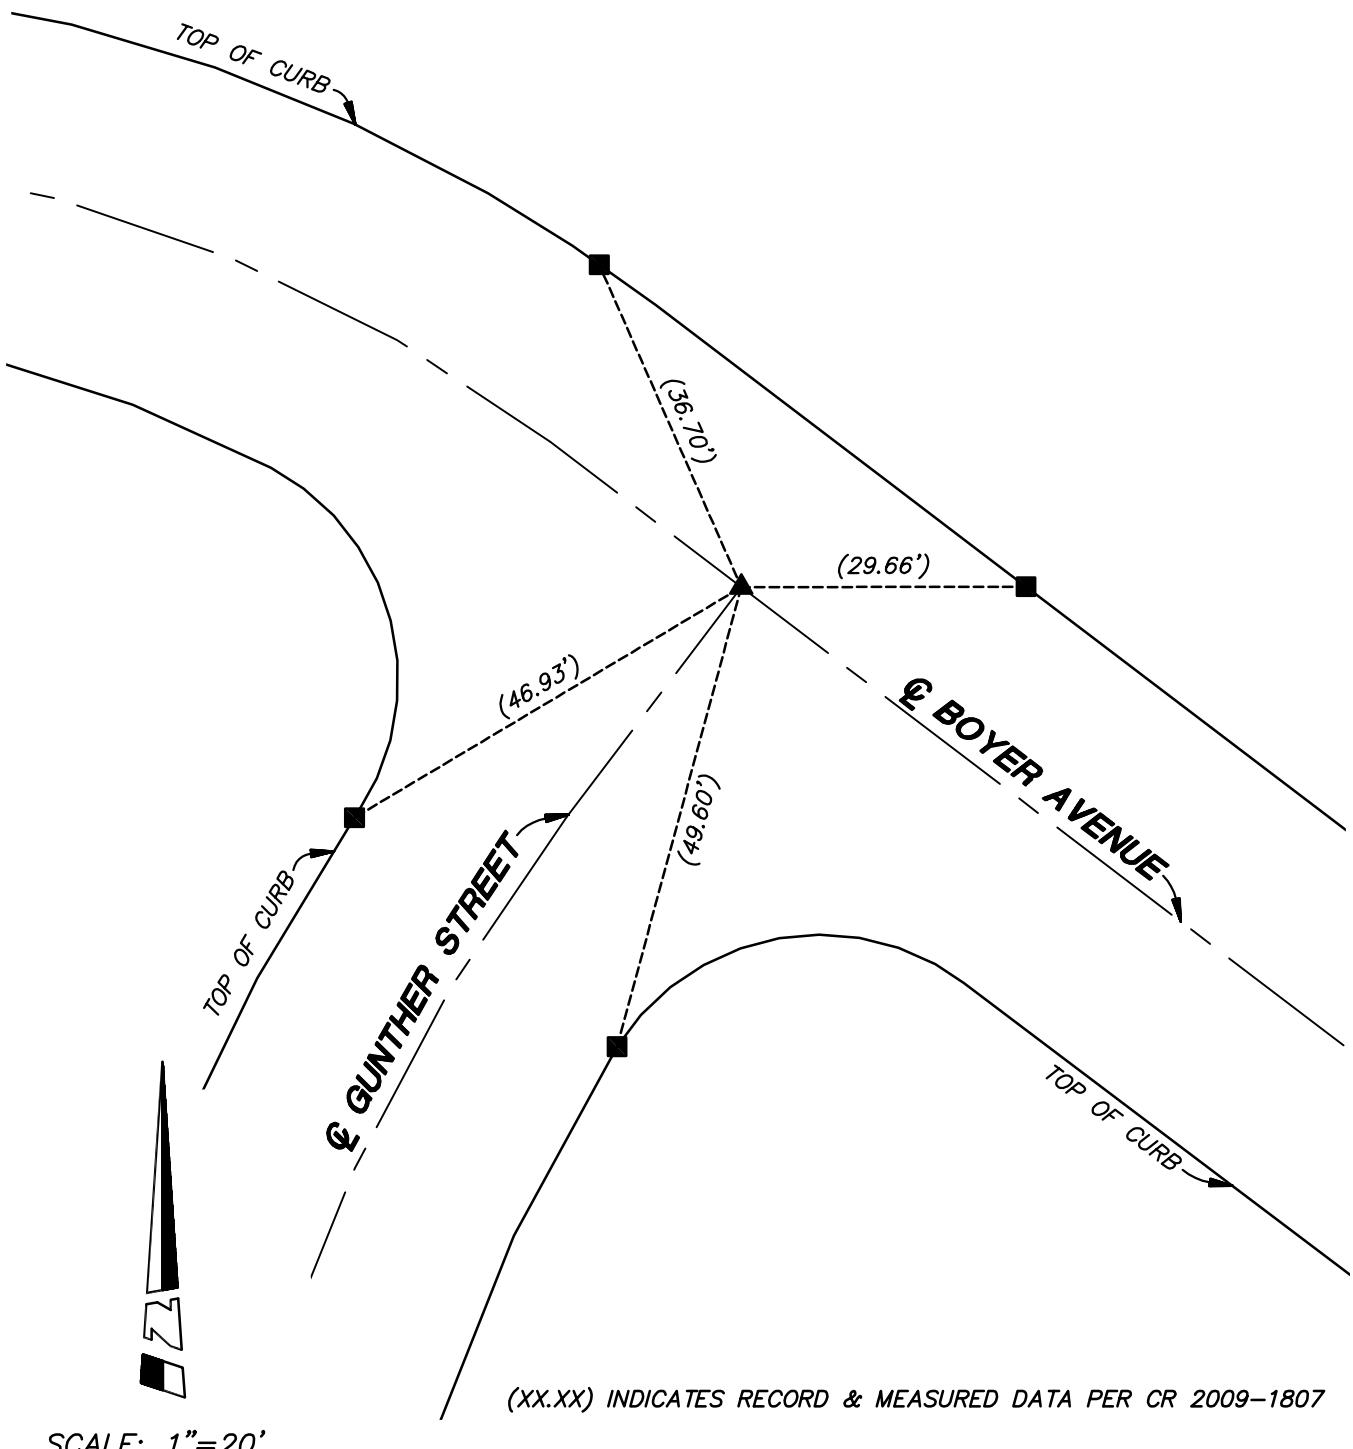

NOTE: THESE TIES ARE FOR THE PURPOSE  
OF PERPETUATING THE FOUND  
MONUMENTATION. NO CLAIM IS MADE AS TO  
THE RELATIONSHIP OF THE POINTS OR LINES  
SHOWN HEREON TO THE TRUE BOUNDARY  
LOCATIONS.

### MONUMENT NOTES

- FOUND CHISELED "X" ON TOP OF CURB PER CR 2009-1807,  
SET LEAD, TACK & TAG "PLS 9305 TIE"
- ▲ FOUND NAIL & TAG, STAMPED "SANTA ANA SURVEY" PER  
CR 2009-1807

# CORNER RECORD

Agency Index


Document Number

2019-0594

City of SANTA ANA

County of ORANGE, California

Brief Legal Description CENTERLINE INTERSECTION OF JACKSON STREET AND BOYER AVENUE

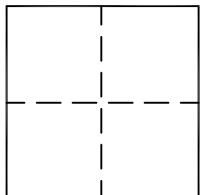

## CORNER TYPE

- Government Corner       Control
- Meander       Property
- Rancho       Other

## COORDINATES (Optional )

N. \_\_\_\_\_ E. \_\_\_\_\_  
 Elevation \_\_\_\_\_  
 Units \_\_\_\_\_ Metric \_\_\_\_\_ U.S. Survey Foot \_\_\_\_\_  
 Horizontal Datum \_\_\_\_\_  
 Zone \_\_\_\_\_ Epoch Date \_\_\_\_\_  
 Vertical Datum \_\_\_\_\_

Date of Survey JULY 18, 2018

- Complies with Public Resources Code §§8801-8819
- Complies with Public Resources Code §§8890-8902

PLS Act Ref:  8765(d)       8771       8773       Other:

Corner/ Monument:	<input checked="" type="checkbox"/> Left as found	<input type="checkbox"/> Established	<input type="checkbox"/> Rebuilt	<input checked="" type="checkbox"/> Pre-Construction
	<input type="checkbox"/> Found and tagged	<input type="checkbox"/> Reestablished	<input type="checkbox"/> Referenced	<input type="checkbox"/> Post-Construction

Narrative of corner identified and monument as found, set, reset, replaced, or removed:

See sheet #2 for description (s):

*THESE TIES ARE FOR THE PURPOSE OF PERPETUATING THE FOUND MONUMENTATION. NO CLAIM IS MADE AS TO THE RELATIONSHIP OF THE POINTS OR LINES SHOWN HEREON TO THE TRUE BOUNDARY LOCATIONS.*

## SURVEYOR'S STATEMENT

This Corner Record was prepared by me or under my direction in conformance with  
the Professional Land Surveyors' Act on SEPTEMBER 17, 2019

Signed Jeffrey J. Lenherr P.L.S. or R.C.E. No. 9305



## COUNTY SURVEYOR'S STATEMENT

This Corner Record was received FEB 4 2019


and examined and filed SEP 27 2019

Signed Kevin R. Hills P.L.S. or R.C.E. No. 6617

Title COUNTY SURVEYOR



County Surveyor's Comment \_\_\_\_\_  
 \_\_\_\_\_  
 \_\_\_\_\_

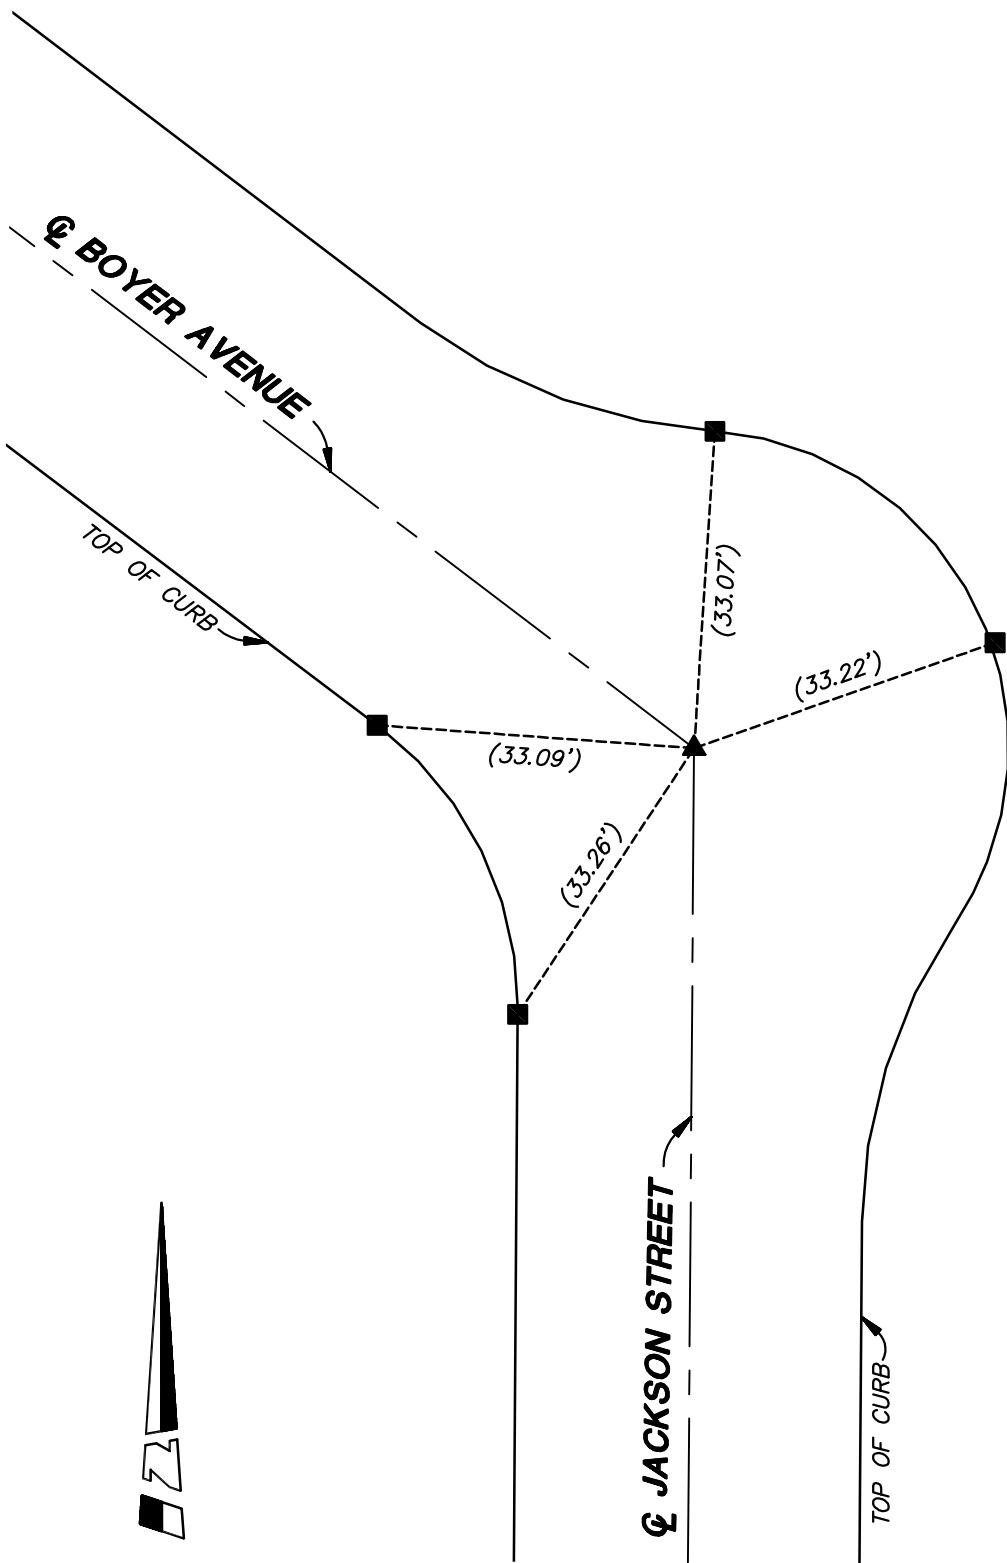

SCALE: 1"=20'

(XX.XX) INDICATES RECORD &amp; MEASURED DATA PER CR 2009-1835

NOTE: THESE TIES ARE FOR THE PURPOSE  
OF PERPETUATING THE FOUND  
MONUMENTATION. NO CLAIM IS MADE AS TO  
THE RELATIONSHIP OF THE POINTS OR LINES  
SHOWN HEREON TO THE TRUE BOUNDARY  
LOCATIONS.

### MONUMENT NOTES

- FOUND CHISELED "X" ON TOP OF CURB PER CR 2009-1835,  
SET LEAD, TACK & TAG "PLS 9305 TIE"
- ▲ FOUND NAIL & CSA TAG PER CR 2009-1835